

CÔNG TY TNHH THƯƠNG MẠI VÀ XÂY DỰNG PV INCONS

Địa chỉ: Số P007, đường Lý Thái Tổ, phường Hưng Phú, Tp. Cần Thơ
Điện thoại: 0772 194 789 MST: 1501112147
Website: www.pvincons.com Email: pvincons@gmail.com

HỒ SƠ THIẾT KẾ

CÔNG TRÌNH: NHÀ Ở


ĐỊA CHỈ: THỪA ĐẤT, TỜ BẢN ĐỒ SỐ, ĐƯỜNG LÊ HỒNG
 PHONG, PHƯỜNG BÌNH THỦY, TP. CẦN THƠ

CHỦ ĐẦU TƯ:

GIAI ĐOẠN: (1) THIẾT KẾ CƠ SỞ



TỶ LỆ / SCALE: **A3 - 1:1** SỐ BẢN VẼ: **SD102**

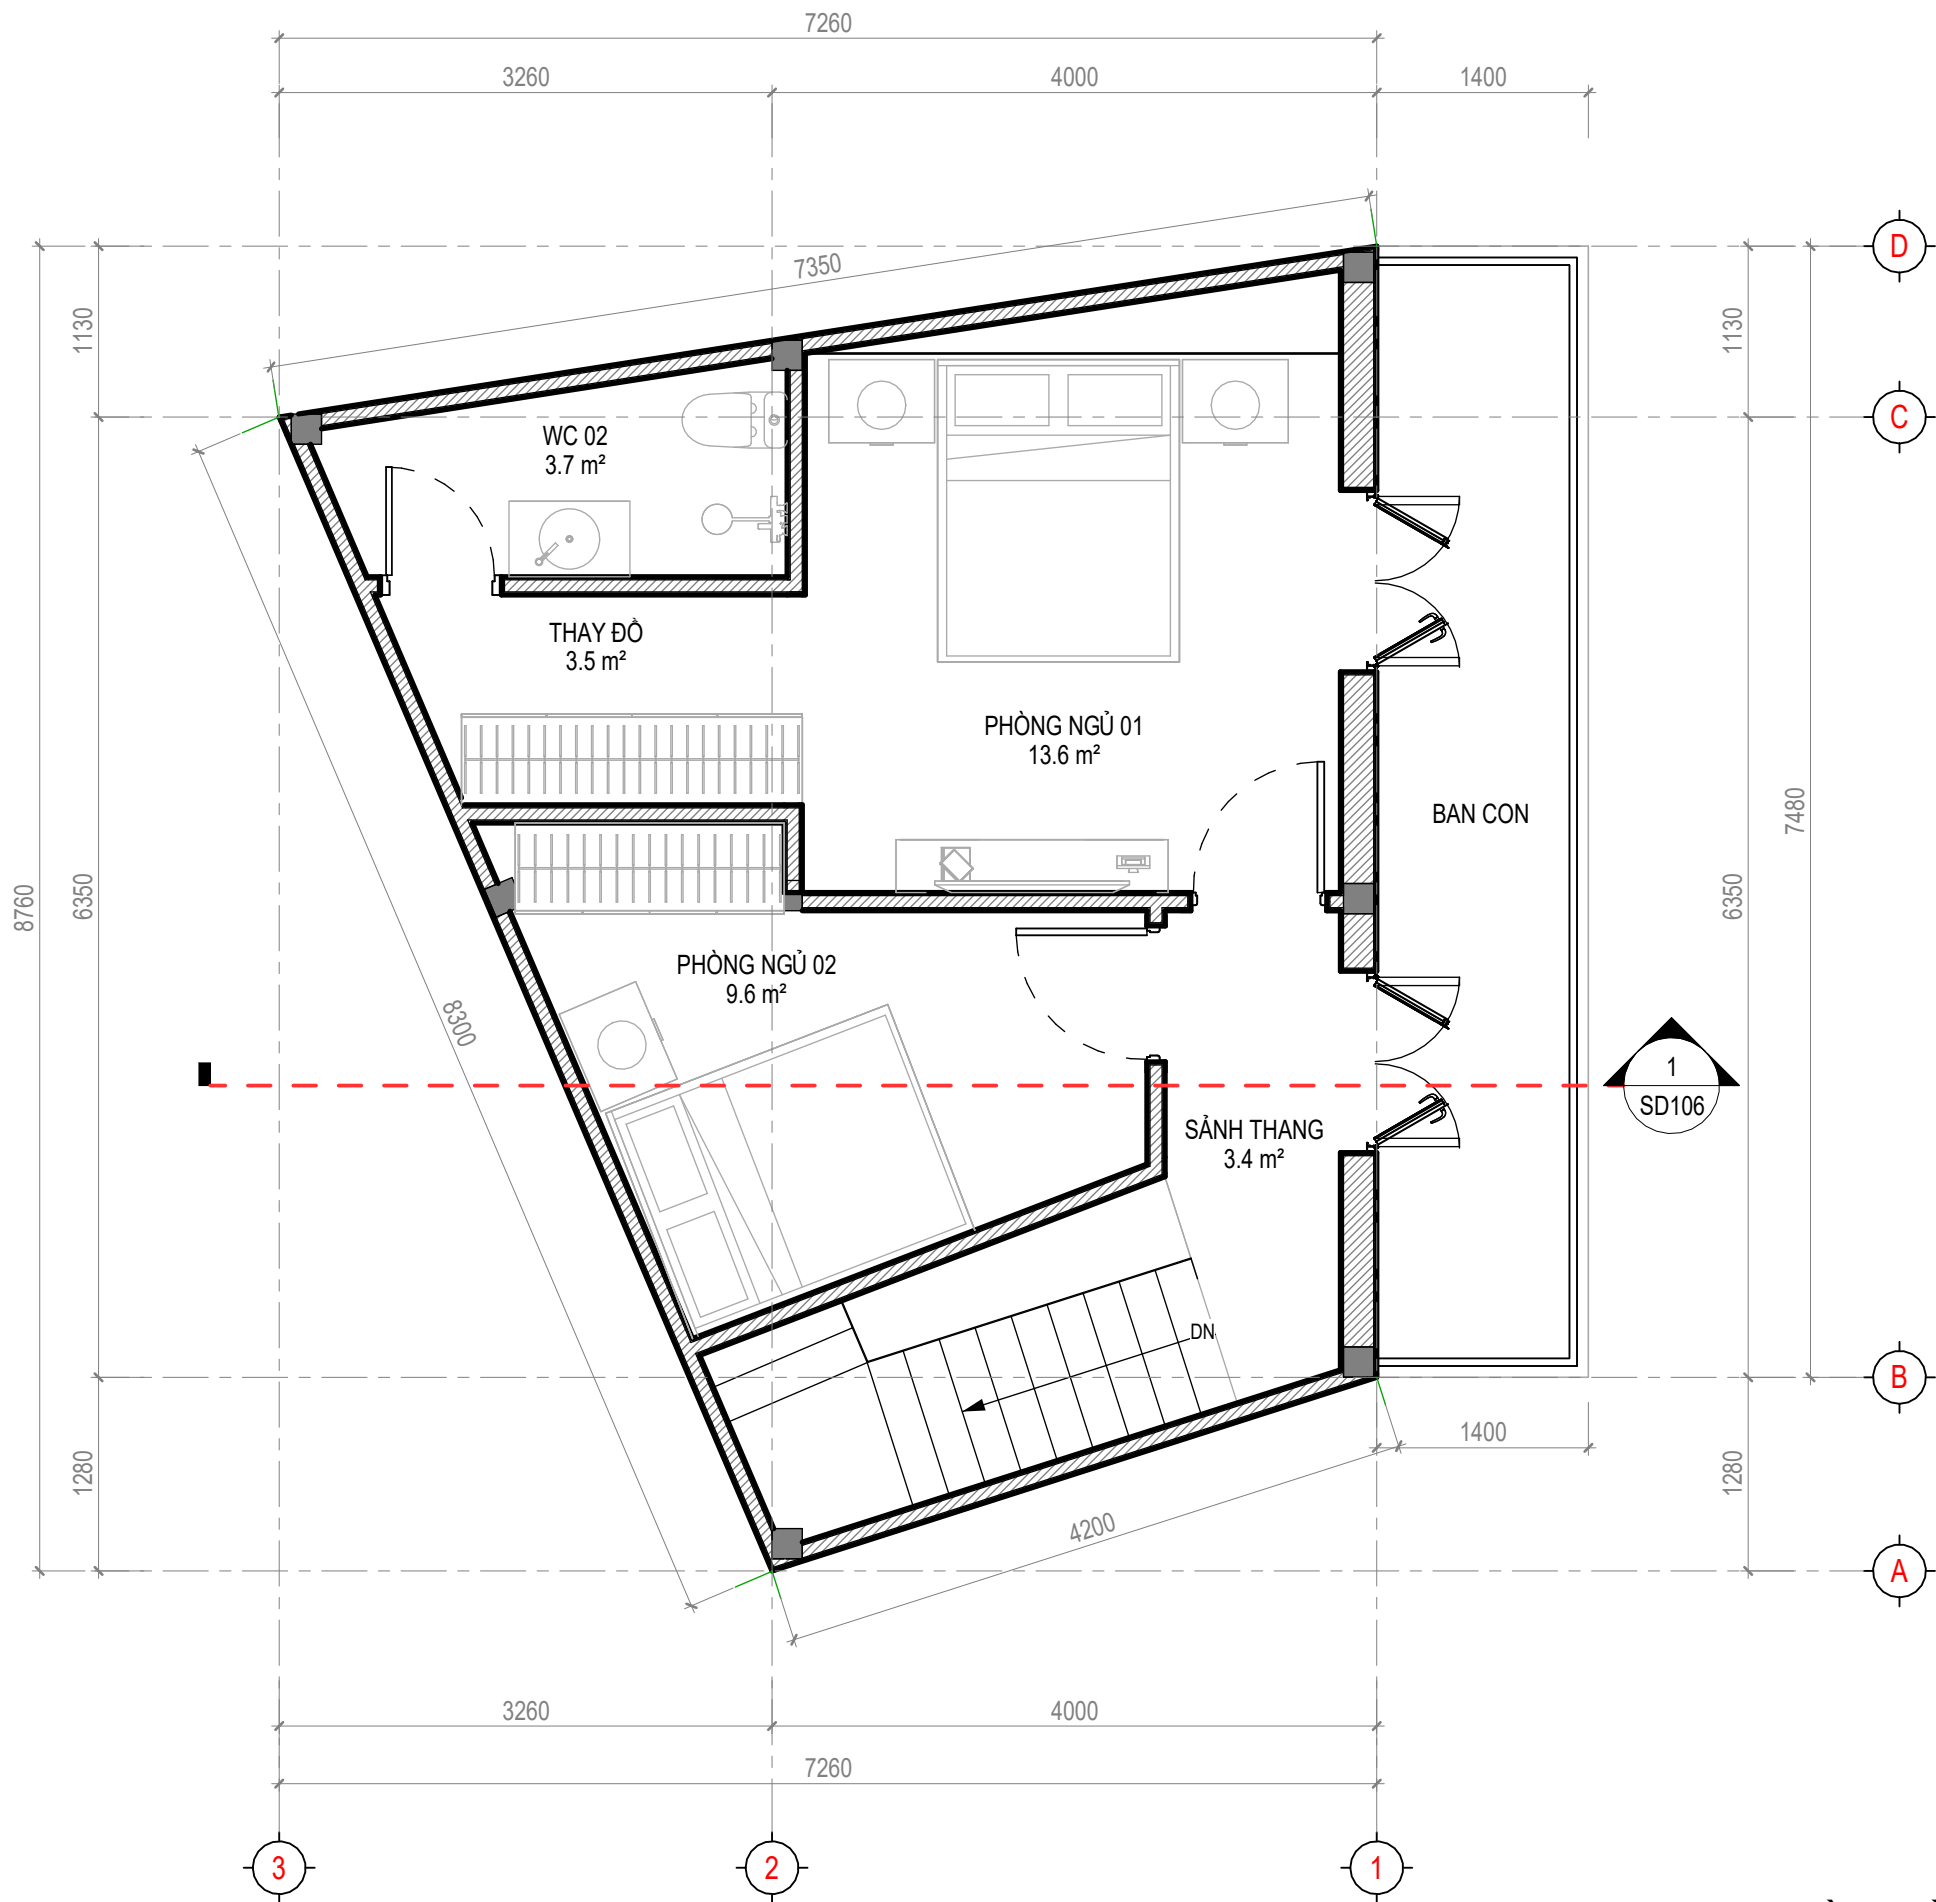

MẶT BẰNG TẦNG 2
TL 1 : 50

LOẠI HỒ SƠ / DOCUMENT STYPE
(1) THIẾT KẾ CƠ SỞ

Toàn bộ hồ sơ thiết kế, bản vẽ, hình ảnh và các nội dung liên quan thuộc quyền sở hữu trí tuệ của Công ty PV Incons. Không được sao chép, sửa đổi, chuyển nhượng hoặc sử dụng cho bất kỳ mục đích nào khác ngoài dự án này mà không có sự đồng ý bằng văn bản của chủ sở hữu bản quyền.

CHỦ ĐẦU TƯ / INVESTOR:

.....

ĐỊA CHỈ / ADDRESS:

THỪA ĐẤT, TỜ BẢN ĐỒ SỐ, ĐƯỜNG LÊ HỒNG PHONG, PHƯỜNG BÌNH THỦY, TP. CẦN THƠ

CÔNG TY TNHH THƯƠNG MẠI VÀ XÂY DỰNG
PV INCONS

Địa chỉ: Số 007, Đường Lý Thái Tổ, P. Hưng Phú, Tp. Cần Thơ

Điện thoại: (+84) 0722 194 789

Email: pvincons@gmail.com

No.	Description	Date

- Bản vẽ thiết kế này chỉ được sử dụng khi đã được đọc, hiểu và kiểm tra bởi kỹ sư có chuyên môn phù hợp.

- Trong quá trình thi công, nếu có bất kỳ sai khác nào giữa bản vẽ thiết kế và thực tế hiện trường, đơn vị thi công phải báo cáo kịp thời cho đơn vị thiết kế và chủ đầu tư để được xem xét, điều chỉnh và phê duyệt trước khi tiếp tục thi công. Mọi sự thay đổi không được phép sẽ không thuộc trách nhiệm của đơn vị thiết kế.

- Kích thước trong bản vẽ là kích thước hoàn thiện, khi thi công cần kết hợp các bản vẽ có liên quan.

CÔNG TRÌNH / PROJECT NAME :

NHÀ Ở

ĐỊA ĐIỂM / LOCATION:

THỪA ĐẤT, TỜ BẢN ĐỒ SỐ, ĐƯỜNG LÊ HỒNG PHONG, PHƯỜNG BÌNH THỦY, TP. CẦN THƠ

HANG MỤC / ITEM:

XÂY DỰNG MỚI

TÊN BẢN VẼ / DRAWING TITLE:


MẶT BẰNG TẦNG 2

SỐ HỢP ĐỒNG: 06/03/2026/PVI-VBTT

NGÀY / DATE: 03/07/26

TỶ LỆ / SCALE: A3 - 1:1

SỐ BẢN VẼ: SD103

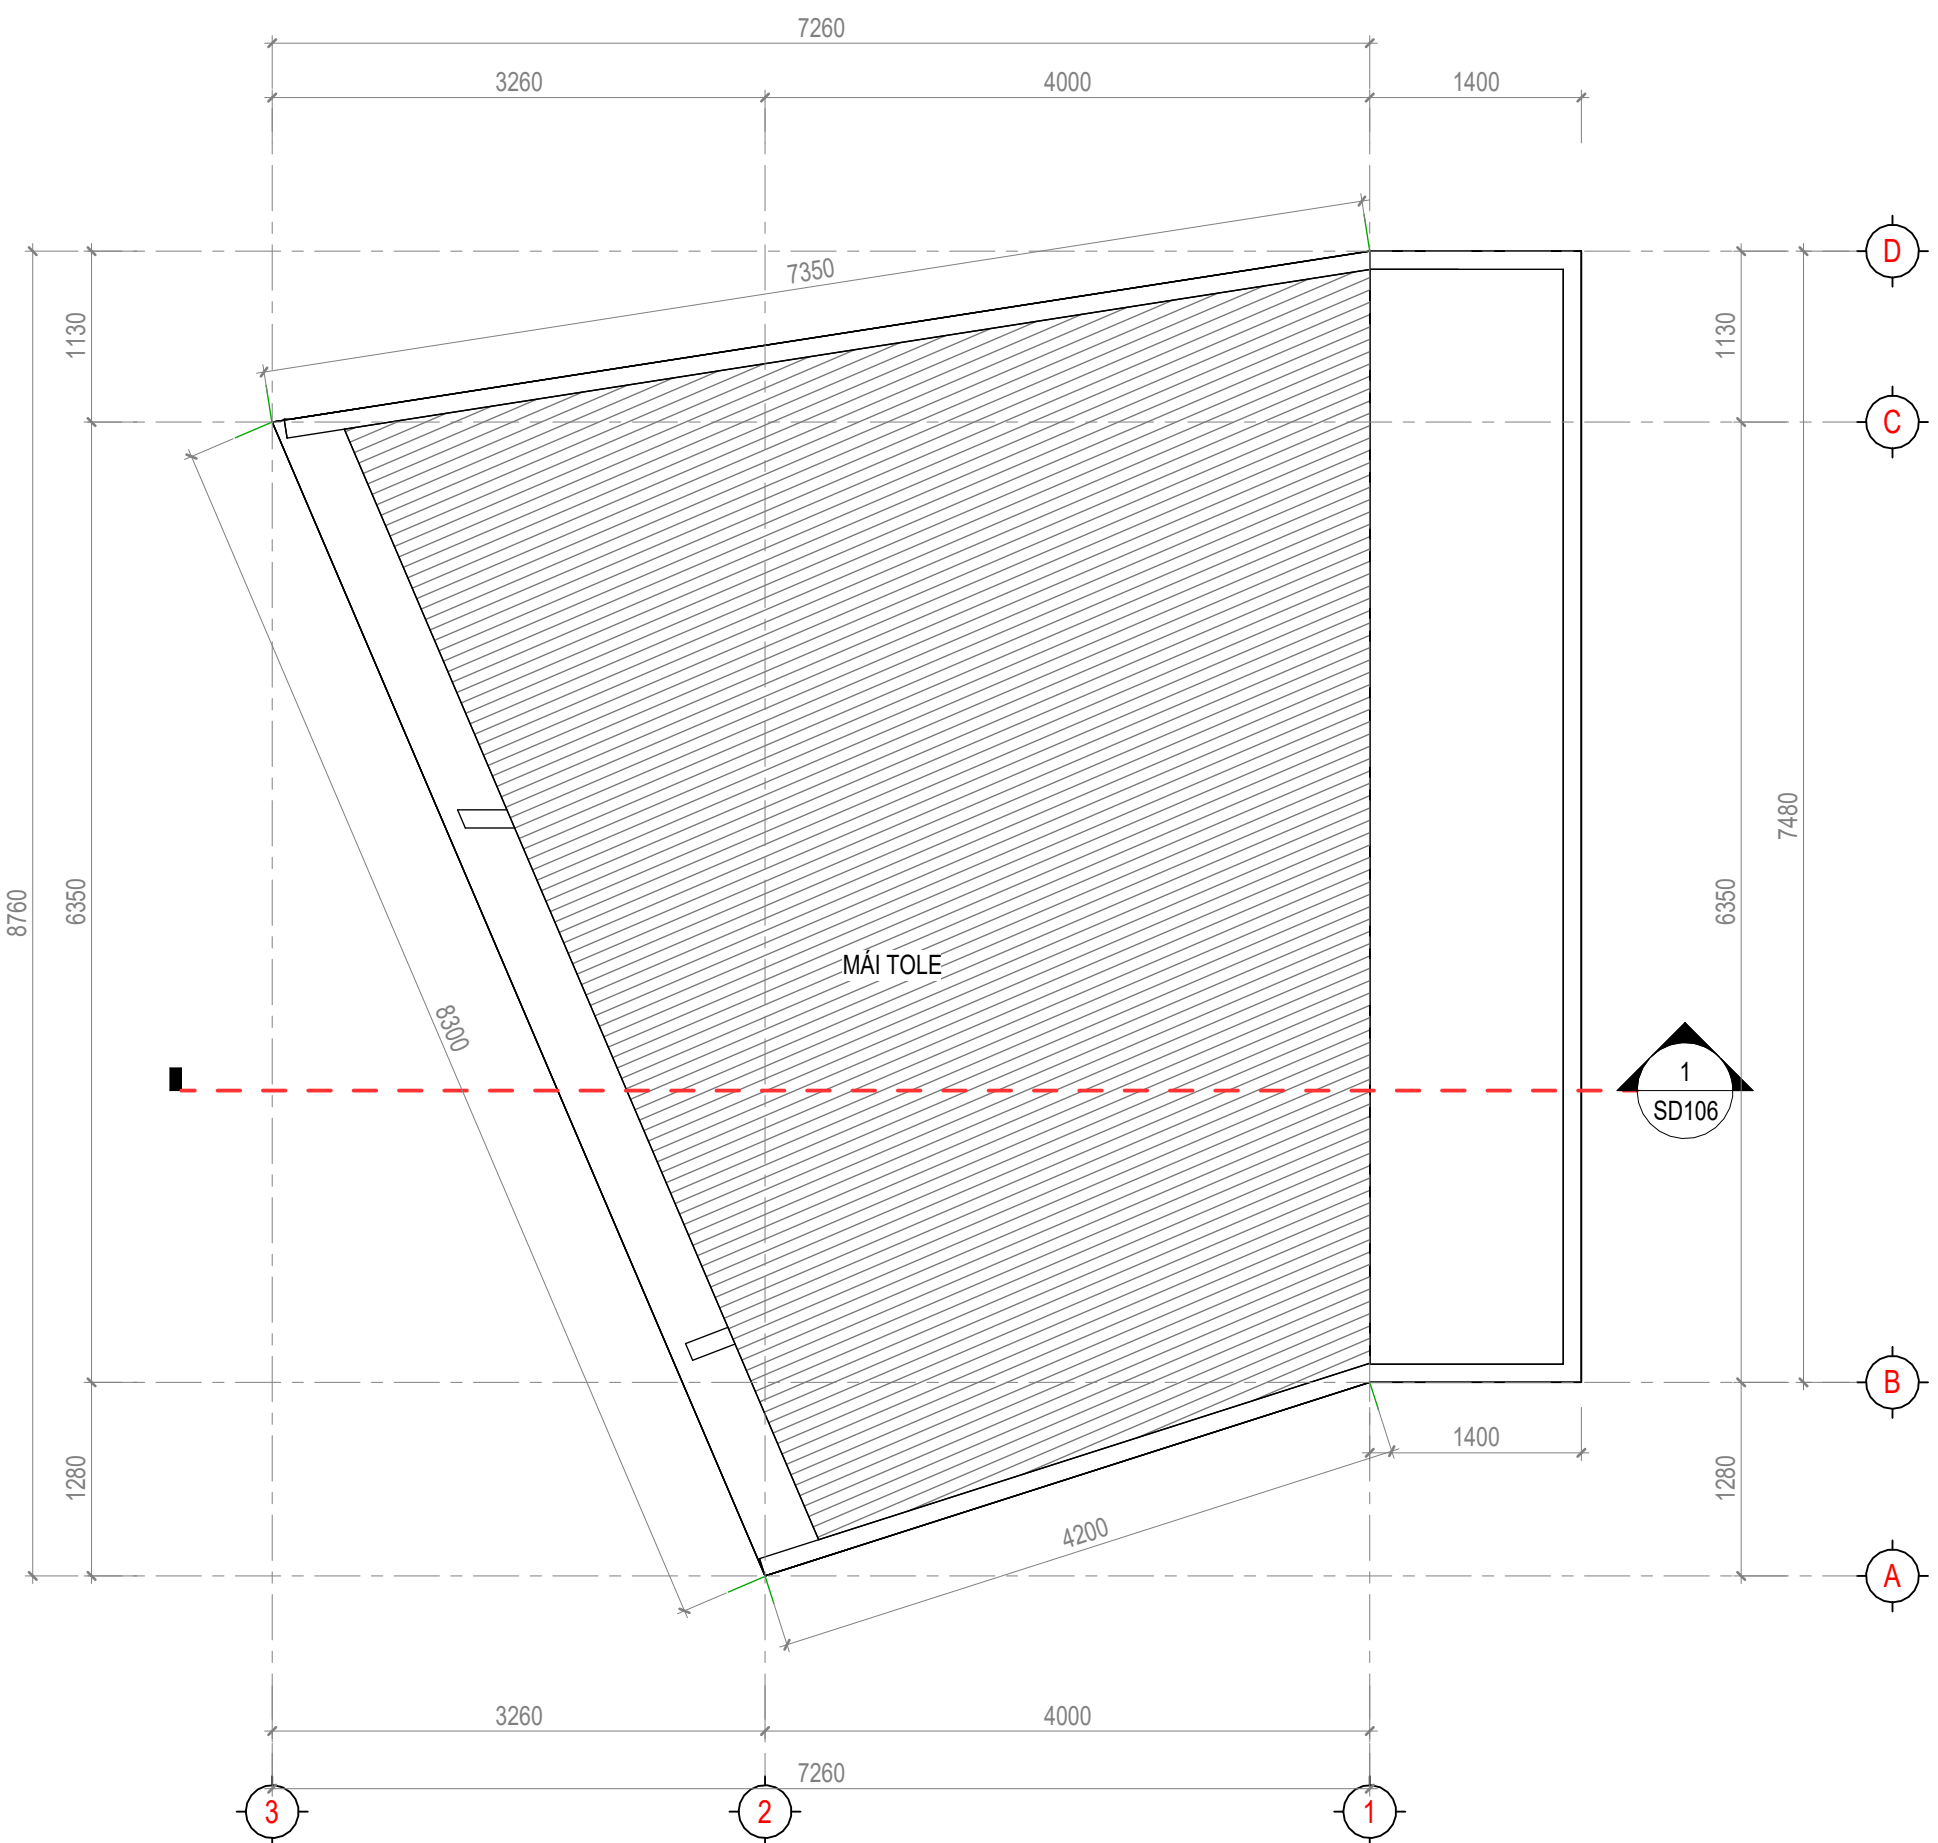

MẶT BẰNG MÁI
TL 1 : 50

LOẠI HỒ SƠ / DOCUMENT STYPE
(1) THIẾT KẾ CƠ SỞ

Toàn bộ hồ sơ thiết kế, bản vẽ, hình ảnh và các nội dung liên quan thuộc quyền sở hữu trí tuệ của Công ty PV Incons. Không được sao chép, sửa đổi, chuyển nhượng hoặc sử dụng cho bất kỳ mục đích nào khác ngoài dự án này mà không có sự đồng ý bằng văn bản của chủ sở hữu bản quyền.

CHỦ ĐẦU TƯ / INVESTOR:

.....

ĐỊA CHỈ / ADDRESS:

THỪA ĐẤT, TỜ BẢN ĐỒ SỐ, ĐƯỜNG LÊ HỒNG PHONG, PHƯỜNG BÌNH THỦY, TP. CẦN THƠ



CÔNG TY TNHH THƯƠNG MẠI VÀ XÂY DỰNG
PV INCONS

Địa chỉ: Số 007, Đường Lý Thái Tổ, P. Hưng Phú, Tp. Cần Thơ
Điện thoại: (+84) 0722 194 789
Email: pvincons@gmail.com

No.	Description	Date

- Bản vẽ thiết kế này chỉ được sử dụng khi đã được đọc, hiểu và kiểm tra bởi kỹ sư có chuyên môn phù hợp.

- Trong quá trình thi công, nếu có bất kỳ sai khác nào giữa bản vẽ thiết kế và thực tế hiện trường, đơn vị thi công phải báo cáo kịp thời cho đơn vị thiết kế và chủ đầu tư để được xem xét, điều chỉnh và phê duyệt trước khi tiếp tục thi công. Mọi sự thay đổi không được phép sẽ không thuộc trách nhiệm của đơn vị thiết kế.

- Kích thước trong bản vẽ là kích thước hoàn thiện, khi thi công cần kết hợp các bản vẽ có liên quan.

CÔNG TRÌNH / PROJECT NAME :

NHÀ Ở

ĐỊA ĐIỂM / LOCATION:

THỪA ĐẤT, TỜ BẢN ĐỒ SỐ, ĐƯỜNG LÊ HỒNG PHONG, PHƯỜNG BÌNH THỦY, TP. CẦN THƠ

HẠNG MỤC / ITEM:

XÂY DỰNG MỚI

TÊN BẢN VẼ / DRAWING TITLE:

MẶT BẰNG MÁI

SỐ HỢP ĐỒNG: 06/03/2026/PVI-VBTT	NGÀY / DATE: 03/07/26
TỶ LỆ / SCALE: A3 - 1:1	SỐ BẢN VẼ: SD104





MẶT CẮT DỌC CÔNG TRÌNH

TL 1 : 50

LOẠI HỒ SƠ / DOCUMENT STYPE

(1) THIẾT KẾ CƠ SỞ

Toàn bộ hồ sơ thiết kế, bản vẽ, hình ảnh và các nội dung liên quan thuộc quyền sở hữu trí tuệ của Công ty PV Incons. Không được sao chép, sửa đổi, chuyển nhượng hoặc sử dụng cho bất kỳ mục đích nào khác ngoài dự án này mà không có sự đồng ý bằng văn bản của chủ sở hữu bản quyền.

CHỦ ĐẦU TƯ / INVESTOR:

DI CHỈ / ADDRESS:

**THỪA ĐẤT, TỜ BẢN ĐỒ SỐ
....., ĐƯỜNG LÊ HỒNG PHONG,
PHƯỜNG BÌNH THỦY, TP. CẦN
THƠ**



ÔNG TY TNHH THƯƠNG MẠI VÀ XÂY DỰNG
PV INCONS

Địa chỉ: Số 007, Đường Lý Thái Tổ,
P. Hưng Phú, Tp. Cần Thơ

Điện thoại: (+84) 0722 194 789

Email: pvincons@gmail.com

[illegible]

Bản vẽ thiết kế này chỉ được sử dụng khi đã được
tọc, hiểu và kiểm tra bởi kỹ sư có chuyên môn phù hợp.

Trong quá trình thi công, nếu có bất kỳ sai khác nào giữa bản vẽ thiết kế và thực tế hiện trường, đơn vị thi công phải báo cáo kịp thời cho đơn vị thiết kế và chủ đầu tư để được xem xét, điều chỉnh và phê duyệt trước khi tiếp tục thi công. Mọi sự thay đổi không được phép sẽ không thuộc trách nhiệm của đơn vị thiết kế.

Kích thước trong bản vẽ là kích thước hoàn thiện, khi thi công cần kết hợp các bản vẽ có liên quan.

ÔNG TRÌNH / PROJECT NAME :

NHÀ Ở

ĐỊA ĐIỂM / LOCATION:

THỦA ĐẤT, TỜ BẢN ĐỒ SỐ
....., ĐƯỜNG LÊ HỒNG PHONG,
PHƯỜNG BÌNH THỦY, TP. CẦN
THƠ'

HANG MỤC / ITEM:

XÂY DỰNG MỚI

TÊN BẢN VẼ / DRAWING TITLE:

MẶT CẮT DỌC CÔNG TRÌNH

SỐ HỢP ĐỒNG:	NGÀY / DATE:
6/03/2026/PVI-VBTT	03/07/26

TỶ LỆ / SCALE: A3 - 1:1	SỐ BẢN VẼ: SD106
-----------------------------------	----------------------------