



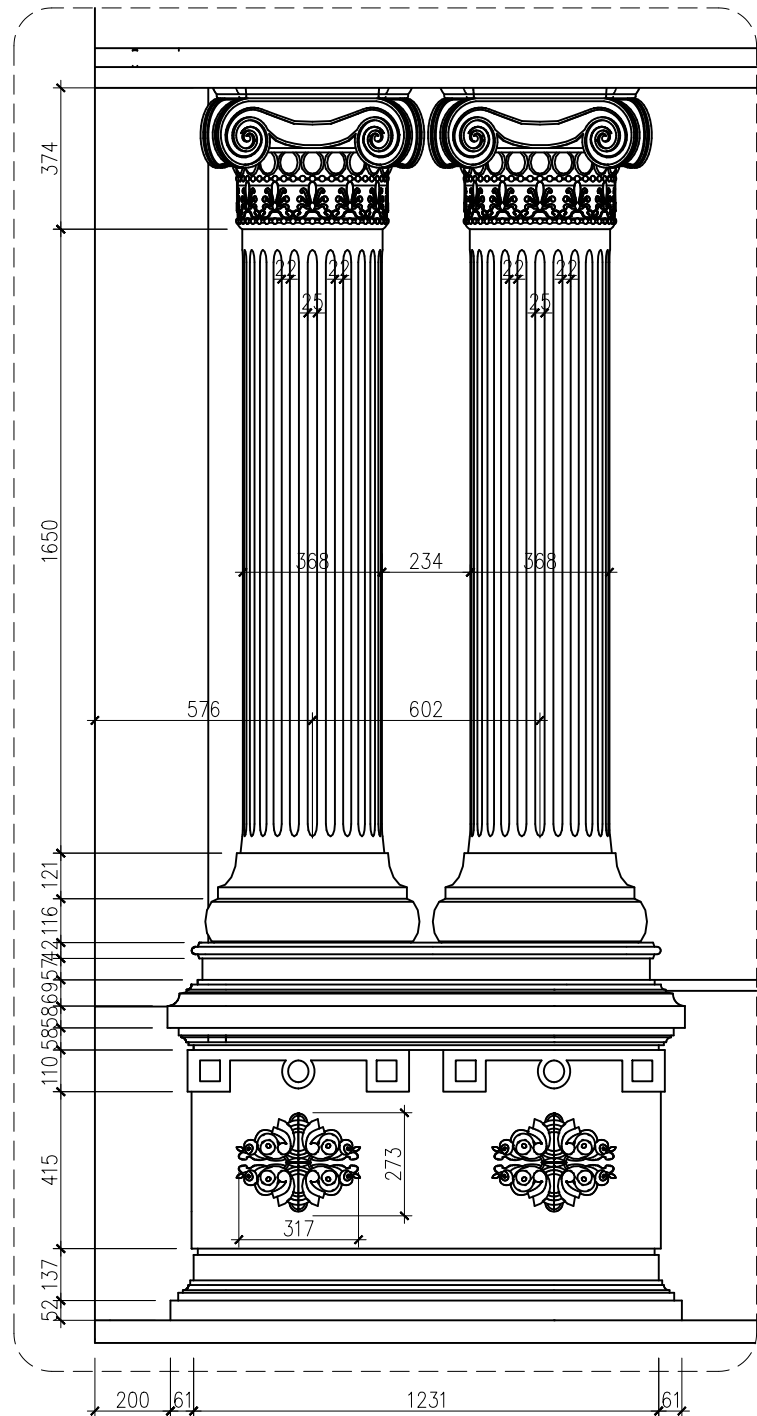

CHI TIẾT 3

TL: 1/20

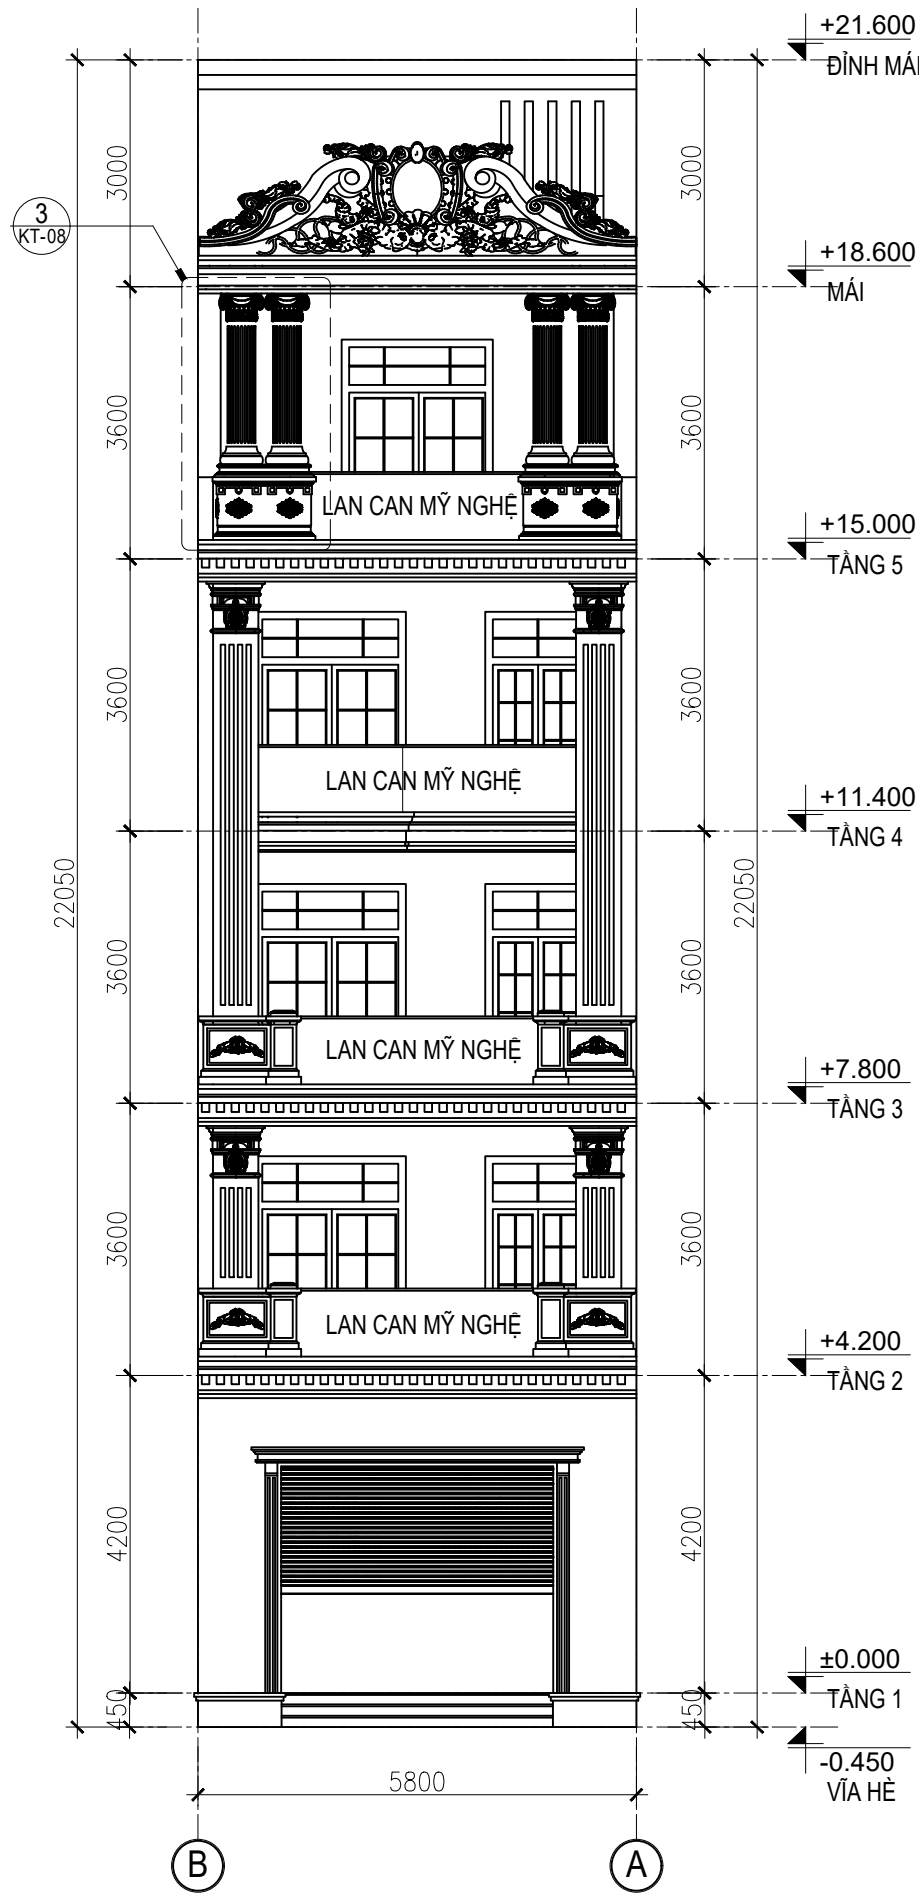

MẶT ĐỨNG TRỤC B-A

TL: 1/100

LOẠI HỒ SƠ / DOCUMENT STYPE

Thiết kế thi công (LOD 350)

Toàn bộ hồ sơ thiết kế, bản vẽ, hình ảnh và các nội dung liên quan thuộc quyền sở hữu trí tuệ của Công ty PV Incons. Không được sao chép, sửa đổi, chuyển nhượng hoặc sử dụng cho bất kỳ mục đích nào khác ngoài dự án này mà không có sự đồng ý bằng văn bản của chủ sở hữu bản quyền.

CHỦ ĐẦU TƯ / INVESTOR:

NGUYỄN HỮU THỪA

ĐỊA CHỈ / ADDRESS:

198, CÁCH MẠNG THÁNG TÁM,
PHƯỜNG BÌNH THỦY, TP. CẦN THƠ



CÔNG TY TNHH THƯƠNG MẠI VÀ XÂY DỰNG
PV INCONS

Địa chỉ: Số 007, Đ. Lý Thái Tổ, KDC.

Hưng Phú I, Q. Cái Răng, TP. Cần Thơ

Điện thoại: (+84) 0772 194 789

Email: pvincons@gmail.com

No.	Description	Date

- Bản vẽ thiết kế này chỉ được sử dụng khi đã được đọc, hiểu và kiểm tra bởi kỹ sư có chuyên môn phù hợp.

- Trong quá trình thi công, nếu có bất kỳ sai khác nào giữa bản vẽ thiết kế và thực tế hiện trường, đơn vị thi công phải báo cáo kịp thời cho đơn vị thiết kế và chủ đầu tư để được xem xét, điều chỉnh và phê duyệt trước khi tiếp tục thi công. Mọi sự thay đổi không được phép sẽ không thuộc trách nhiệm của đơn vị thiết kế.

- Đơn vị thi công phải lập bản vẽ Shop Drawing (LOD 400) cho các chi tiết kỹ thuật và trình duyệt trước khi triển khai.

- Kích thước trong bản vẽ là kích thước hoàn thiện, khi thi công cần kết hợp các bản vẽ có liên quan.

CÔNG TRÌNH / PROJECT NAME:

NHÀ Ở KẾT HỢP VĂN PHÒNG LÀM VIỆC

ĐỊA ĐIỂM / LOCATION:

198, CÁCH MẠNG THÁNG TÁM,
PHƯỜNG BÌNH THỦY, TP. CẦN THƠ

HẠNG MỤC / ITEM:

CẢI TẠO MẶT TIỀN

TÊN BẢN VẼ / DRAWING TITLE:

SHEETTITLE

SỐ HỢP ĐỒNG

09/2026/HĐTK

TỶ LỆ / SCALE:

1:100

HOÀN THÀNH

.../09/2026

SỐ BẢN VẼ:

KT-08 /...