

CÔNG TY TNHH THƯƠNG MẠI VÀ XÂY DỰNG PV INCONS

Địa chỉ: Số P007, đường Lý Thái Tổ, phường Hưng Phú, Tp. Cần Thơ
Điện thoại: 0772 194 789 MST: 1501112147
Website: www.pvincons.com Email: pvincons@gmail.com

HỒ SƠ THIẾT KẾ

CÔNG TRÌNH: NHÀ Ở KẾT HỢP VĂN PHÒNG LÀM VIỆC

ĐỊA CHỈ: THỪA ĐẤT 296, TỜ BẢN ĐỒ SỐ 90, SỐ 198, Đ. CÁCH MẠNG THÁNG
TÁM, P. BÙI HỮU NGHĨA, Q. BÌNH THỦY, TP. CẦN THƠ

CHỦ ĐẦU TƯ: NGUYỄN HỮU THỪA

GIAI ĐOẠN: (3) THIẾT KẾ THI CÔNG

21/09/2026



THUYẾT MINH CẢI TẠO CÔNG TRÌNH:

VIỆC CẢI TẠO ĐƯỢC THỰC HIỆN DỰA TRÊN NGUYÊN TẮC: AN TOÀN KẾT CẤU - TỐI ƯU CÔNG NĂNG - ĐẢM BẢO VỆ SINH MÔI TRƯỜNG.

GIẢI ĐOẠN 1: KHẢO SÁT & ĐÁNH GIÁ HIỆN TRẠNG (EXISTING STATUS)

- ĐÂY LÀ BƯỚC QUAN TRỌNG NHẤT ĐỂ XÁC ĐỊNH "SỨC KHỎE" CỦA CÔNG TRÌNH TRƯỚC KHI CAN THIỆP.
- KHẢO SÁT KẾT CẤU: KIỂM TRA HỆ THỐNG DẦM, CỘT, SÀN HIỆN HỮU BẰNG PHƯƠNG PHÁP QUAN TRÁC VẾT NỨT HOẶC SIÊU ÂM CỘT THÉP (NEU CẦN). XÁC ĐỊNH CÁC VỊ TRÍ CHỊU LỰC CHÍNH KHÔNG ĐƯỢC PHÉP XÂM PHẠM.
- HỆ THỐNG KỸ THUẬT (MEP): RÀ SOÁT SƠ ĐỒ ĐIỆN, NƯỚC, INTERNET NGẦM. ĐÁNH GIÁ KHẢ NĂNG TÁI SỬ DỤNG HOẶC THAY THẾ HOÀN TOÀN ĐỂ TRÁNH RÒ RỈ SAU NÀY.
- TRÁC ĐẠC: ĐO ĐẠC LẠI KÍCH THƯỚC THỰC TẾ SO VỚI BẢN VẼ CŨ ĐỂ ĐIỀU CHỈNH SAI LỆCH TRONG THIẾT KẾ MỚI.
- CÔNG TÁC CHUẨN BỊ: LẮP ĐẶT HỆ THỐNG BAO CHE, BIỂN BÁO AN TOÀN VÀ KHU VỰC TẬP KẾT VẬT TƯ TẠM THỜI.

GIẢI ĐOẠN 2: PHÁ DỠ & GIẢI PHÓNG KHÔNG GIAN MẶT BẰNG (DEMOLITION)

- GIẢI ĐOẠN NÀY ĐÒI HỜI SỰ CÂN TRỌNG CAO ĐỂ KHÔNG ẢNH HƯỞNG ĐẾN CÁC KHU VỰC LÂN CẬN VÀ KẾT CẤU CHUNG.
- NGUYÊN TẮC PHÁ DỠ: THỰC HIỆN TỪ TRÊN XUỐNG DƯỚI, TỪ NGOÀI VÀO TRONG. PHÁ DỠ CÁC CẤU KIỆN PHI KẾT CẤU (TƯỜNG NGẮN, TRẦN THẠCH CAO, SÀN GẠCH) TRƯỚC.
- BIỆN PHÁP KỸ THUẬT: SỬ DỤNG MÁY ĐỤC, MÁY CẮT CÀM TAY ĐỂ HẠN CHẾ RUNG CHẤN MẠNH. ĐỐI VỚI CÁC MẢNG TƯỜNG LỚN, PHẢI CẮT NHỎ TRƯỚC KHI HẠ HẠ ĐỂ ĐẢM BẢO AN TOÀN.
- XỬ LÝ PHÉ THẢI: THU GOM XÁ BẦN VÀO BAO TẢI, VẬN CHUYỂN BẰNG THANG MÁY CHUYỂN DỤNG HOẶC VẬN THĂNG RA ĐIỂM TẬP KẾT. ĐẢM BẢO TỰỚI NƯỚC CHỐNG BỤI TRONG SUỐT QUÁ TRÌNH THỰC HIỆN.
- BẢO VỆ TÀI SẢN: CHE CHẮN CÁC THIẾT BỊ HOẶC KHU VỰC KHÔNG CẢI TẠO BẰNG BẠT VÀ GỖ VÁN.

GIẢI ĐOẠN 3: XÂY DỰNG MỚI & LẮP ĐẶT THIẾT BỊ (NEW CONSTRUCTION)

- SAU KHI CÓ MẶT BẰNG "SẠCH", VIỆC THI CÔNG ĐƯỢC TRIỂN KHAI THEO BẢN VẼ THIẾT KẾ MỚI.
- XÂY DỰNG CƠ BẢN: XÂY TƯỜNG NGẮN PHÒNG, CÁN NỀN TẠO DỐC, THI CÔNG CÁC HỆ THỐNG CHỊU LỰC BỔ SUNG (NEU CÓ TẦNG QUY MÔ).
- LẮP ĐẶT HỆ THỐNG MEP: ĐI ỐNG ÂM TƯỜNG CHO HỆ THỐNG ĐIỆN, NƯỚC, ĐIỀU HÒA KHÔNG KHÍ. VIỆC NÀY PHẢI HOÀN THÀNH TRƯỚC KHI TRÁT TƯỜNG VÀ ĐÓNG TRẦN.
- CHÔNG THẨM: ĐÂY LÀ BƯỚC THEN CHÓT TRONG CẢI TẠO. THỰC HIỆN CHÔNG THẨM KỸ LƯỢNG KHU VỰC VỆ SINH, BAN CÔNG VÀ MÁI BẰNG CÁC VẬT LIỆU CHUYÊN DỤNG (SIKA, MÀNG KHÔ...).
- LẮP ĐẶT TRẦN & VÁCH: THI CÔNG KHUNG XƯƠNG THẠCH CAO, LẮP ĐẶT CÁC HẸ CỬA SỔ, CỬA ĐI.

GIẢI ĐOẠN 4: HOÀN THIỆN & BÀN GIAO (COMPLETION)

- GIẢI ĐOẠN TẠO NỀN DIỆN MẠO THẨM MỸ CHO CÔNG TRÌNH.
- CÔNG TÁC ỐP LÁT: ỐP ĐÁ, LÁT GẠCH SÀN THEO CỘT CAO ĐỘ ĐÃ ĐỊNH VỊ. ĐẢM BẢO ĐỘ PHẪNG VÀ MẠCH GẠCH ĐỀU ĐẸP.
- SƠN BẢ & TRANG TRÍ: BẢ MATIT, SƠN LÓT VÀ SƠN PHỦ HOÀN THIỆN. LẮP ĐẶT CÁC VÁCH TRANG TRÍ, GIẤY DÁN TƯỜNG (NEU CÓ).
- LẮP ĐẶT THIẾT BỊ: GẮN CÁC THIẾT BỊ VỆ SINH, THIẾT BỊ ĐIỆN (ĐÈN, Ổ CẮM), TỦ BẾP VÀ ĐỒ NỘI THẤT LIÊN TƯỜNG.
- VỆ SINH CÔNG NGHIỆP: TỔNG VỆ SINH TOÀN BỘ CÔNG TRÌNH, KHỬ MÙI SƠN MỚI VÀ KIỂM TRA VẬN HÀNH THỦ Ỡ HỆ THỐNG (COMMISSIONING) TRƯỚC KHI BÀN GIAO CHO CHỦ ĐẦU TƯ.

LƯU Ý QUAN TRỌNG:

GIẢI ĐOẠN	RỦI RO CHÍNH	GIẢI PHÁP KIỂM SOÁT
HIỆN TRẠNG	SAI LỆCH KÍCH THƯỚC	ĐO ĐẠC 3D HOẶC THỦ CÔNG KỸ LƯỢNG
PHÁ DỠ	RUNG CHẤN, BỤI, ÒN	SỬ DỤNG MÁY CẮT CHUYÊN DỤNG, LƯỚI BAO CHE
XÂY MỚI	THẨM DỘT, CHẬP ĐIỆN	THỦ Ỡ ÁP LỰC NƯỚC VÀ KIỂM TRA MẠCH ĐIỆN KỸ
HOÀN THIỆN	TRẦY XƯỚC, SAI MÀU SƠN	BẢO VỆ BỀ MẶT SAU KHI LẮP ĐỒ NỘI THẤT

LOẠI HỒ SƠ / DOCUMENT STYPE

Thiết kế thi công (LOD 350)

Toàn bộ hồ sơ thiết kế, bản vẽ, hình ảnh và các nội dung liên quan thuộc quyền sở hữu trí tuệ của Công ty PV Incons. Không được sao chép, sửa đổi, chuyển nhượng hoặc sử dụng cho bất kỳ mục đích nào khác ngoài dự án này mà không có sự đồng ý bằng văn bản của chủ sở hữu bản quyền.

CHỦ ĐẦU TƯ / INVESTOR:

NGUYỄN HỮU THỪA

ĐỊA CHỈ / ADDRESS:

198, CÁCH MẠNG THÁNG TÁM,
PHƯỜNG BÌNH THỦY, TP. CẦN THƠ



CÔNG TY TNHH THƯƠNG MẠI VÀ XÂY DỰNG
PV INCONS

Địa chỉ: Số 007, Đ. Lý Thái Tổ, KDC.
Hưng Phú I, Q. Cái Răng, TP. Cần Thơ
Điện thoại: (+84) 0772 194 789
Email: pvincons@gmail.com

No.	Description	Date

- Bản vẽ thiết kế này chỉ được sử dụng khi đã được đọc, hiểu và kiểm tra bởi kỹ sư có chuyên môn phù hợp.

- Trong quá trình thi công, nếu có bất kỳ sai khác nào giữa bản vẽ thiết kế và thực tế hiện trường, đơn vị thi công phải báo cáo kịp thời cho đơn vị thiết kế và chủ đầu tư để được xem xét, điều chỉnh và phê duyệt trước khi tiếp tục thi công. Mọi sự thay đổi không được phép sẽ không thuộc trách nhiệm của đơn vị thiết kế.

- Đơn vị thi công phải lập bản vẽ Shop Drawing (LOD 400) cho các chi tiết kỹ thuật và trình duyệt trước khi triển khai.

- Kích thước trong bản vẽ là kích thước hoàn thiện, khi thi công cần kết hợp các bản vẽ có liên quan.

CÔNG TRÌNH / PROJECT NAME:

NHÀ Ở KẾT HỢP VĂN PHÒNG LÀM VIỆC

ĐỊA ĐIỂM / LOCATION:

198, CÁCH MẠNG THÁNG TÁM,
PHƯỜNG BÌNH THỦY, TP. CẦN THƠ


HANG MỤC / ITEM:

CẢI TẠO MẶT TIỀN

TÊN BẢN VẼ / DRAWING TITLE:

SHEETTITLE

SỐ HỢP ĐỒNG 09/2026/HĐTK	HOÀN THÀNH .../09/2026
TỶ LỆ / SCALE: 1:100	SỐ BẢN VẼ: KT-01 /...

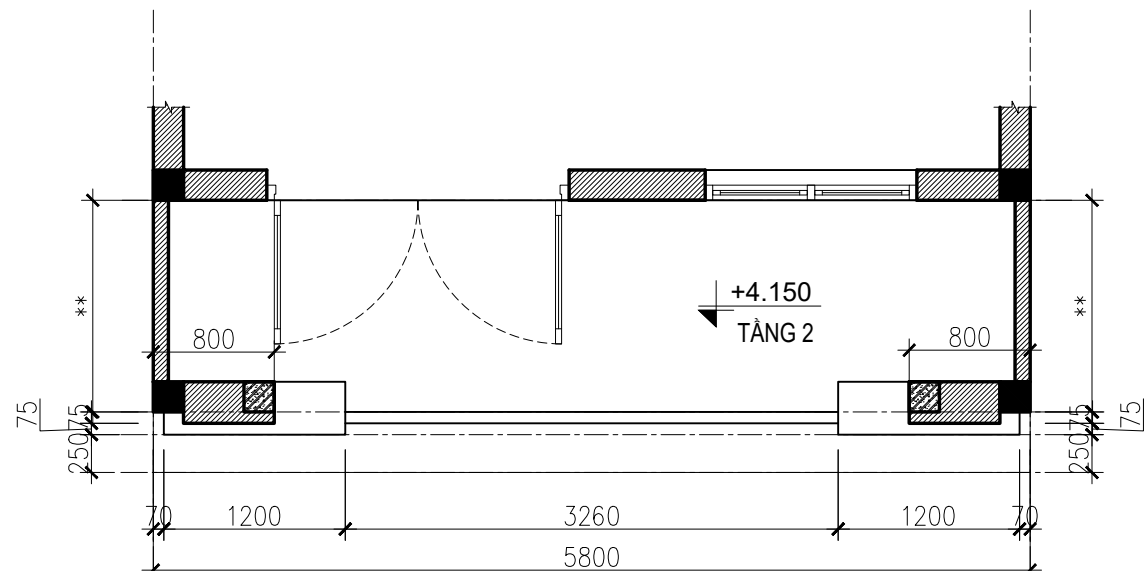


BAN CON TẦNG 2

TL: 1/100

** KÍCH THƯỚC HIỆN HỮU

■ CỘT BÊ TÔNG CỘT THÉP ĐỒ MỚI

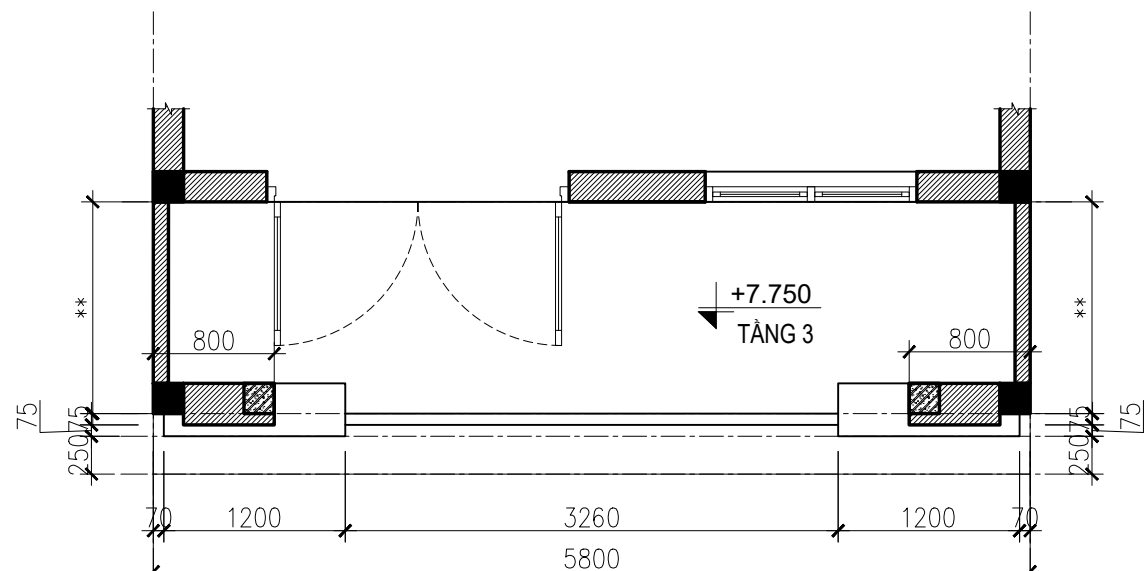


BAN CON TẦNG 3

TL: 1/100

** KÍCH THƯỚC HIỆN HỮU

■ CỘT BÊ TÔNG CỘT THÉP ĐỒ MỚI

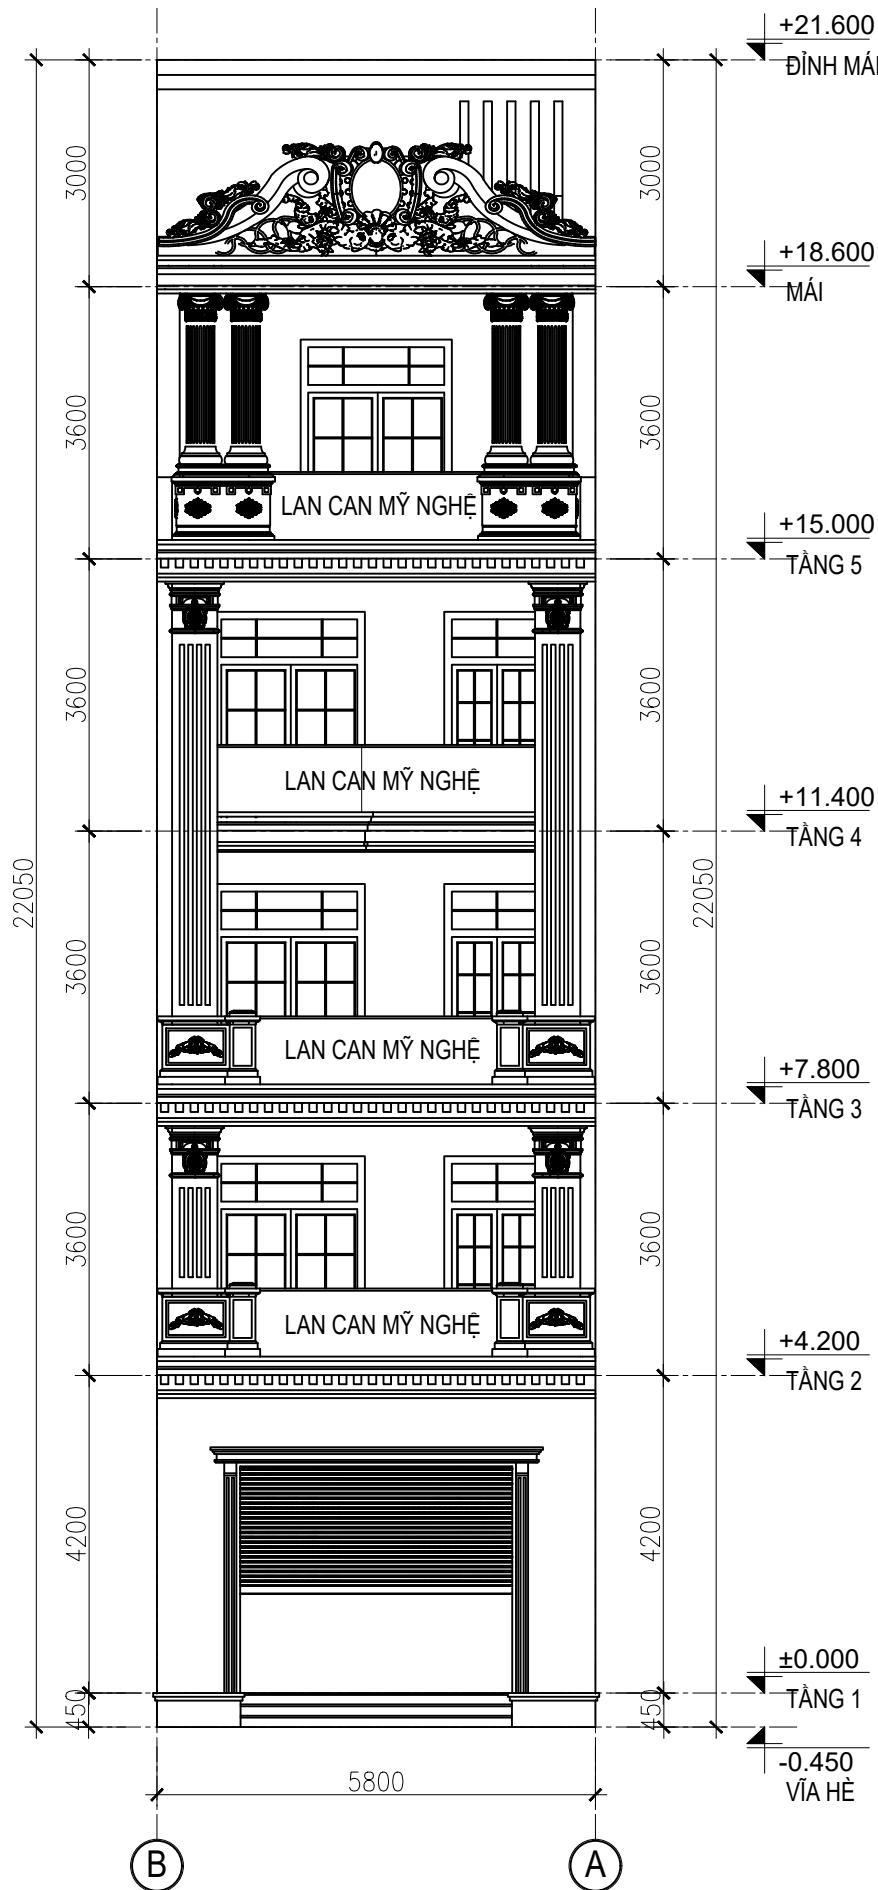

MẶT ĐỨNG TRỰC B-A

TL: 1/100

LOẠI HỒ SƠ / DOCUMENT TYPE

Thiết kế thi công (LOD 350)

Toàn bộ hồ sơ thiết kế, bản vẽ, hình ảnh và các nội dung liên quan thuộc quyền sở hữu trí tuệ của Công ty PV Incons. Không được sao chép, sửa đổi, chuyển nhượng hoặc sử dụng cho bất kỳ mục đích nào khác ngoài dự án này mà không có sự đồng ý bằng văn bản của chủ sở hữu bản quyền.

CHỦ ĐẦU TƯ / INVESTOR:

NGUYỄN HỮU THỪA

ĐỊA CHỈ / ADDRESS:

198, CÁCH MẠNG THÁNG TÁM,
PHƯỜNG BÌNH THỦY, TP. CẦN THƠ


CÔNG TY TNHH THƯƠNG MẠI VÀ XÂY DỰNG
PV INCONS

Địa chỉ: Số 007, Đ. Lý Thái Tổ, KDC.

Hưng Phú I, Q. Cái Răng, TP. Cần Thơ

Điện thoại: (+84) 0772 194 789

Email: pvincons@gmail.com

No.	Description	Date

- Bản vẽ thiết kế này chỉ được sử dụng khi đã được đọc, hiểu và kiểm tra bởi kỹ sư có chuyên môn phù hợp.

- Trong quá trình thi công, nếu có bất kỳ sai khác nào giữa bản vẽ thiết kế và thực tế hiện trường, đơn vị thi công phải báo cáo kịp thời cho đơn vị thiết kế và chủ đầu tư để được xem xét, điều chỉnh và phê duyệt trước khi tiếp tục thi công. Mọi sự thay đổi không được phép sẽ không thuộc trách nhiệm của đơn vị thiết kế.

- Đơn vị thi công phải lập bản vẽ Shop Drawing (LOD 400) cho các chi tiết kỹ thuật và trình duyệt trước khi triển khai.

- Kích thước trong bản vẽ là kích thước hoàn thiện, khi thi công cần kết hợp các bản vẽ có liên quan.

CÔNG TRÌNH / PROJECT NAME:

NHÀ Ở KẾT HỢP VĂN PHÒNG LÀM VIỆC

ĐỊA ĐIỂM / LOCATION:

198, CÁCH MẠNG THÁNG TÁM,
PHƯỜNG BÌNH THỦY, TP. CẦN THƠ

HANG MỤC / ITEM:

CẢI TẠO MẶT TIỀN

TÊN BẢN VẼ / DRAWING TITLE:

SHEETTITLE

SỐ HỢP ĐỒNG

09/2026/HĐTK

TỶ LỆ / SCALE:


1:100

HOÀN THÀNH

.../09/2026

SỐ BẢN VẼ:

KT-02 /...

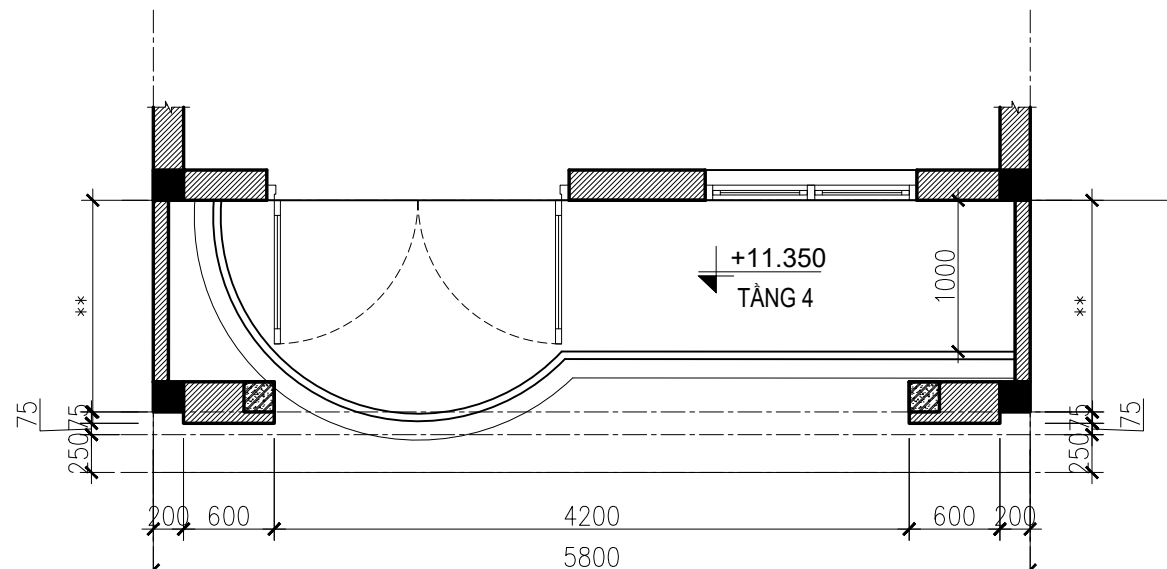


BAN CON TẦNG 4

TL: 1/100

** KÍCH THƯỚC HIỆN HỮU

■ CỘT BÊ TÔNG CỘT THÉP ĐỒ MỚI

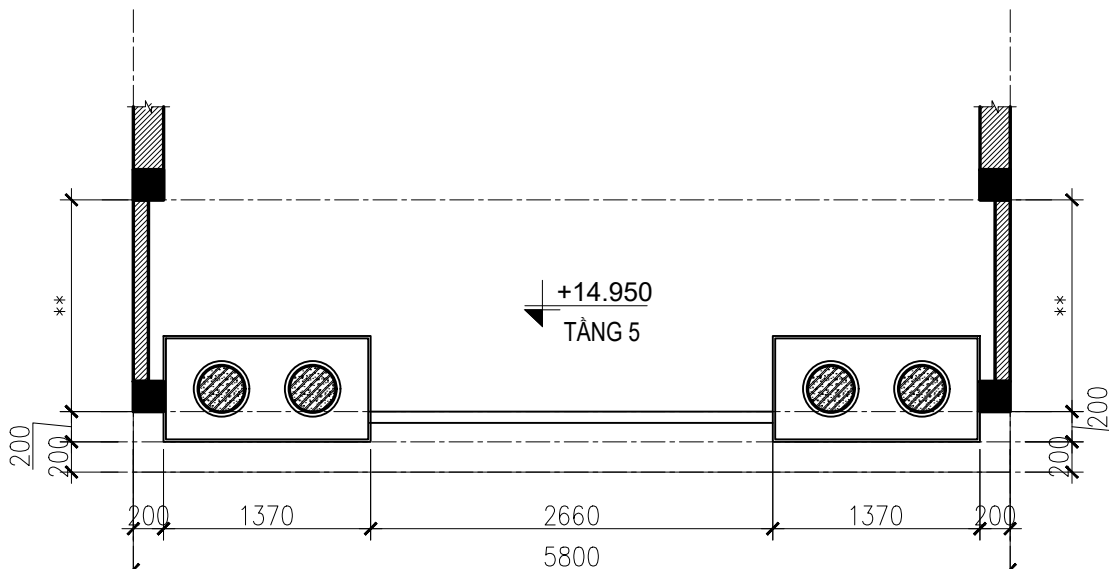


BAN CON TẦNG 5

TL: 1/100

** KÍCH THƯỚC HIỆN HỮU

● CỘT BÊ TÔNG CỘT THÉP ĐỒ MỚI

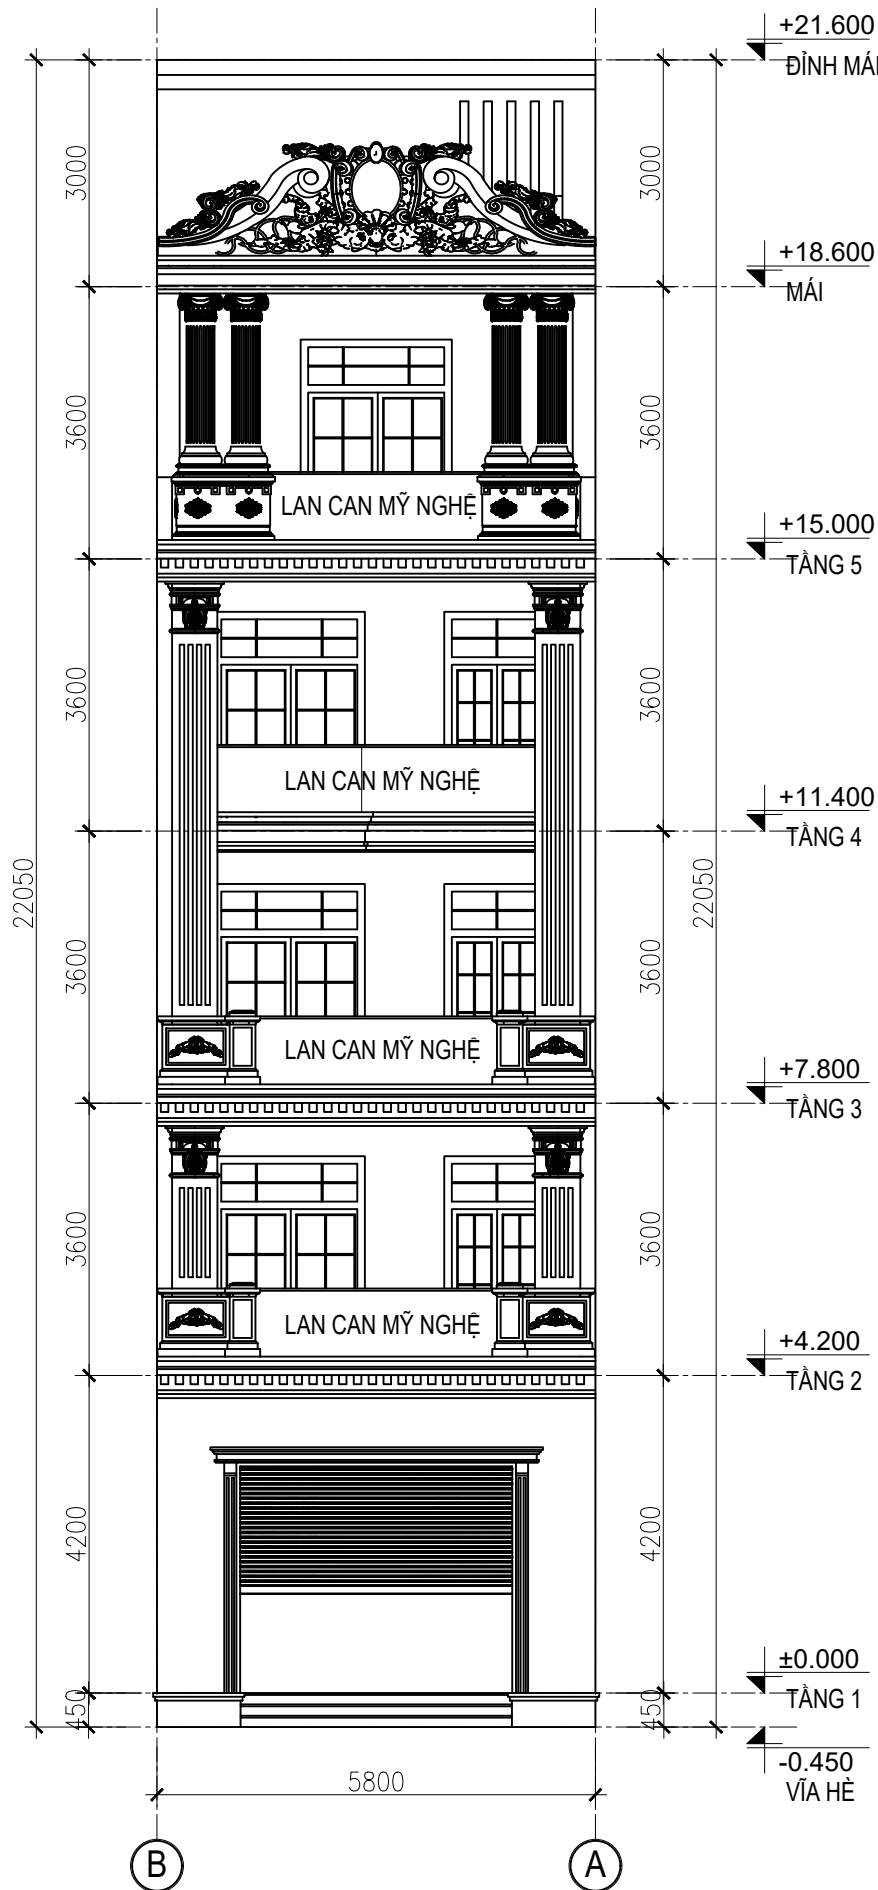

MẶT ĐỨNG TRỰC B-A

TL: 1/100

LOẠI HỒ SƠ / DOCUMENT TYPE

Thiết kế thi công (LOD 350)

Toàn bộ hồ sơ thiết kế, bản vẽ, hình ảnh và các nội dung liên quan thuộc quyền sở hữu trí tuệ của Công ty PV Incons. Không được sao chép, sửa đổi, chuyển nhượng hoặc sử dụng cho bất kỳ mục đích nào khác ngoài dự án này mà không có sự đồng ý bằng văn bản của chủ sở hữu bản quyền.

CHỦ ĐẦU TƯ / INVESTOR:

NGUYỄN HỮU THỪA

ĐỊA CHỈ / ADDRESS:

198, CÁCH MẠNG THÁNG TÁM,
PHƯỜNG BÌNH THỦY, TP. CẦN THƠ



Địa chỉ: Số 007, Đ. Lý Thái Tổ, KDC.
Hưng Phú I, Q. Cái Răng, TP. Cần Thơ
Điện thoại: (+84) 0772 194 789
Email: pvincons@gmail.com

No.	Description	Date

- Bản vẽ thiết kế này chỉ được sử dụng khi đã được đọc, hiểu và kiểm tra bởi kỹ sư có chuyên môn phù hợp.

- Trong quá trình thi công, nếu có bất kỳ sai khác nào giữa bản vẽ thiết kế và thực tế hiện trường, đơn vị thi công phải báo cáo kịp thời cho đơn vị thiết kế và chủ đầu tư để được xem xét, điều chỉnh và phê duyệt trước khi tiếp tục thi công. Mọi sự thay đổi không được phép sẽ không thuộc trách nhiệm của đơn vị thiết kế.

- Đơn vị thi công phải lập bản vẽ Shop Drawing (LOD 400) cho các chi tiết kỹ thuật và trình duyệt trước khi triển khai.

- Kích thước trong bản vẽ là kích thước hoàn thiện, khi thi công cần kết hợp các bản vẽ có liên quan.

CÔNG TRÌNH / PROJECT NAME:

NHÀ Ở KẾT HỢP VĂN PHÒNG LÀM VIỆC

ĐỊA ĐIỂM / LOCATION:

198, CÁCH MẠNG THÁNG TÁM,
PHƯỜNG BÌNH THỦY, TP. CẦN THƠ


HẠNG MỤC / ITEM:

CẢI TẠO MẶT TIỀN

TÊN BẢN VẼ / DRAWING TITLE:

SHEETTITLE


SỐ HỢP ĐỒNG 09/2026/HĐTK	HOÀN THÀNH .../09/2026
TỶ LỆ / SCALE: 1:100	SỐ BẢN VẼ: KT-03 /...

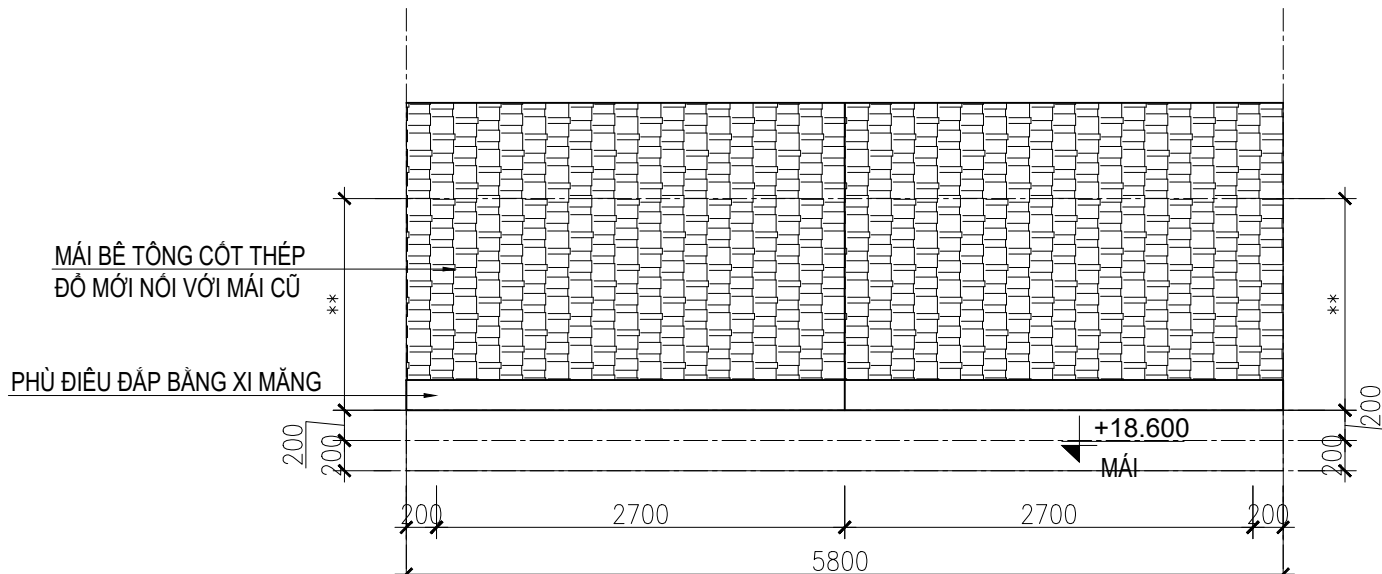

** KÍCH THƯỚC HIỆN HỮU

MẶT BẰNG MÁI

TL: 1/100

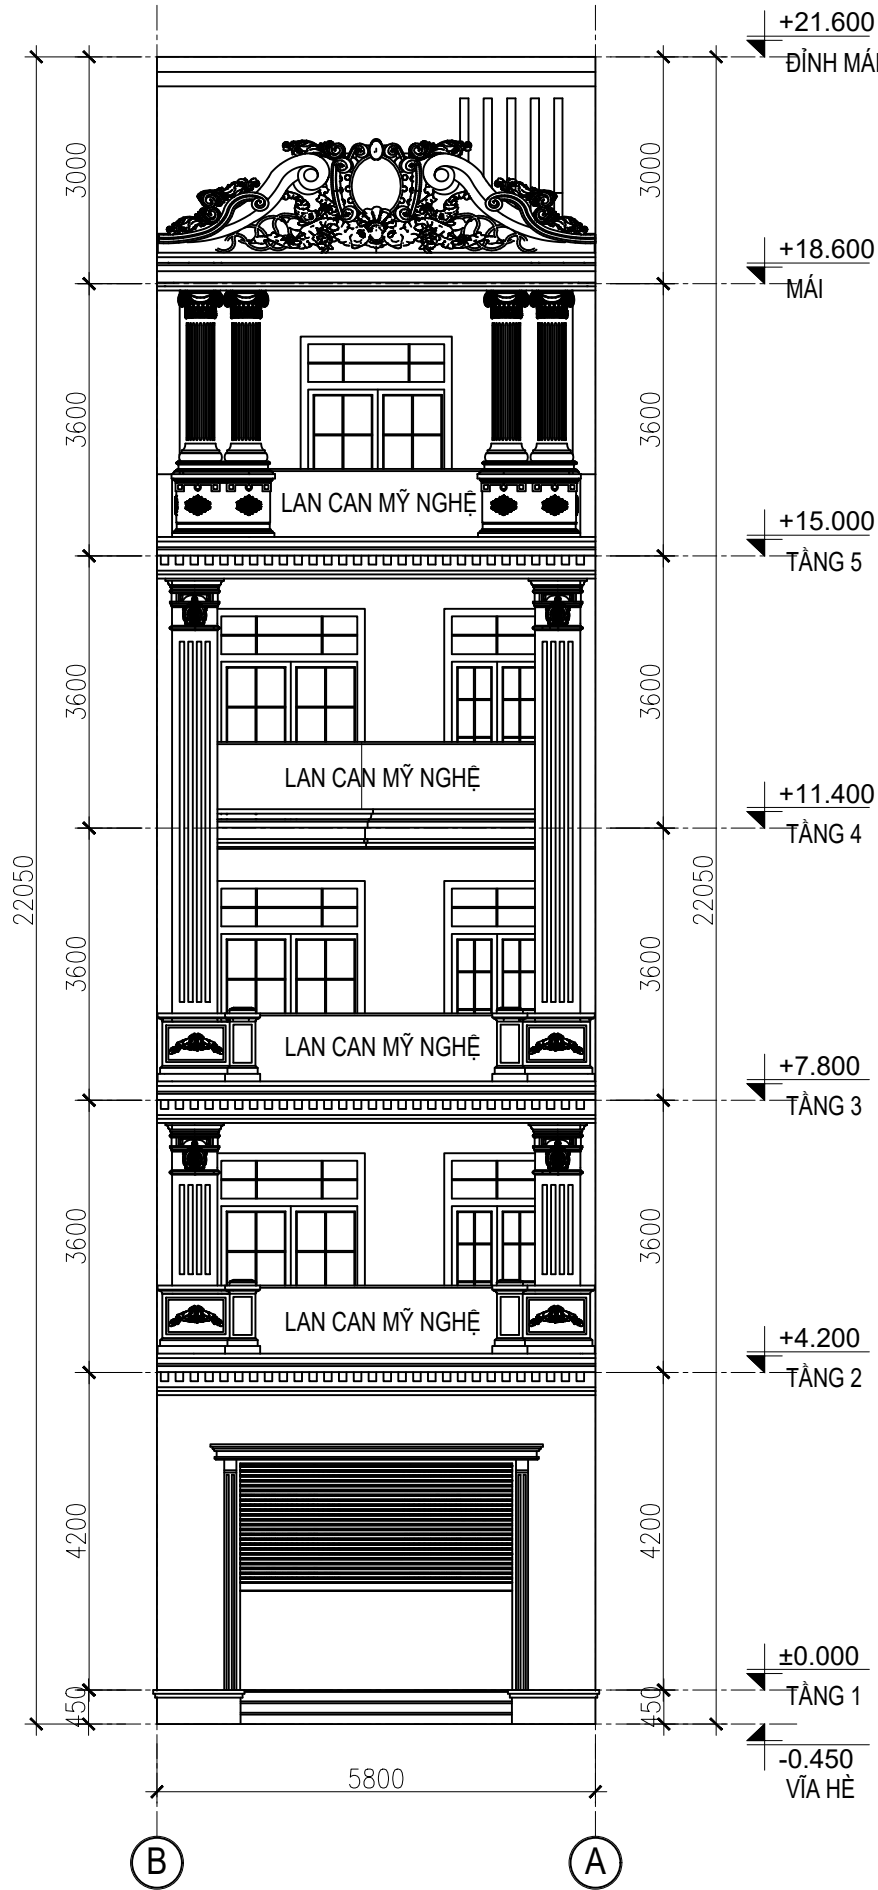

MẶT ĐỨNG TRỰC B-A

TL: 1/100

LOẠI HỒ SƠ / DOCUMENT TYPE

Thiết kế thi công (LOD 350)

Toàn bộ hồ sơ thiết kế, bản vẽ, hình ảnh và các nội dung liên quan thuộc quyền sở hữu trí tuệ của Công ty PV Incons. Không được sao chép, sửa đổi, chuyển nhượng hoặc sử dụng cho bất kỳ mục đích nào khác ngoài dự án này mà không có sự đồng ý bằng văn bản của chủ sở hữu bản quyền.

CHỦ ĐẦU TƯ / INVESTOR:

NGUYỄN HỮU THỪA

ĐỊA CHỈ / ADDRESS:

198, CÁCH MẠNG THÁNG TÁM,
PHƯỜNG BÌNH THỦY, TP. CẦN THƠ



Địa chỉ: Số 007, Đ. Lý Thái Tổ, KDC.
Hưng Phú I, Q. Cái Răng, TP. Cần Thơ
Điện thoại: (+84) 0772 194 789
Email: pvincons@gmail.com

No.	Description	Date

- Bản vẽ thiết kế này chỉ được sử dụng khi đã được đọc, hiểu và kiểm tra bởi kỹ sư có chuyên môn phù hợp.

- Trong quá trình thi công, nếu có bất kỳ sai khác nào giữa bản vẽ thiết kế và thực tế hiện trường, đơn vị thi công phải báo cáo kịp thời cho đơn vị thiết kế và chủ đầu tư để được xem xét, điều chỉnh và phê duyệt trước khi tiếp tục thi công. Mọi sự thay đổi không được phép sẽ không thuộc trách nhiệm của đơn vị thiết kế.

- Đơn vị thi công phải lập bản vẽ Shop Drawing (LOD 400) cho các chi tiết kỹ thuật và trình duyệt trước khi triển khai.

- Kích thước trong bản vẽ là kích thước hoàn thiện, khi thi công cần kết hợp các bản vẽ có liên quan.

CÔNG TRÌNH / PROJECT NAME:

NHÀ Ở KẾT HỢP VĂN PHÒNG LÀM VIỆC

ĐỊA ĐIỂM / LOCATION:

198, CÁCH MẠNG THÁNG TÁM,
PHƯỜNG BÌNH THỦY, TP. CẦN THƠ


HẠNG MỤC / ITEM:

CẢI TẠO MẶT TIỀN

TÊN BẢN VẼ / DRAWING TITLE:

SHEETTITLE

SỐ HỢP ĐỒNG 09/2026/HĐTK	HOÀN THÀNH .../09/2026
TỶ LỆ / SCALE: 1:100	SỐ BẢN VẼ: KT-04 /...

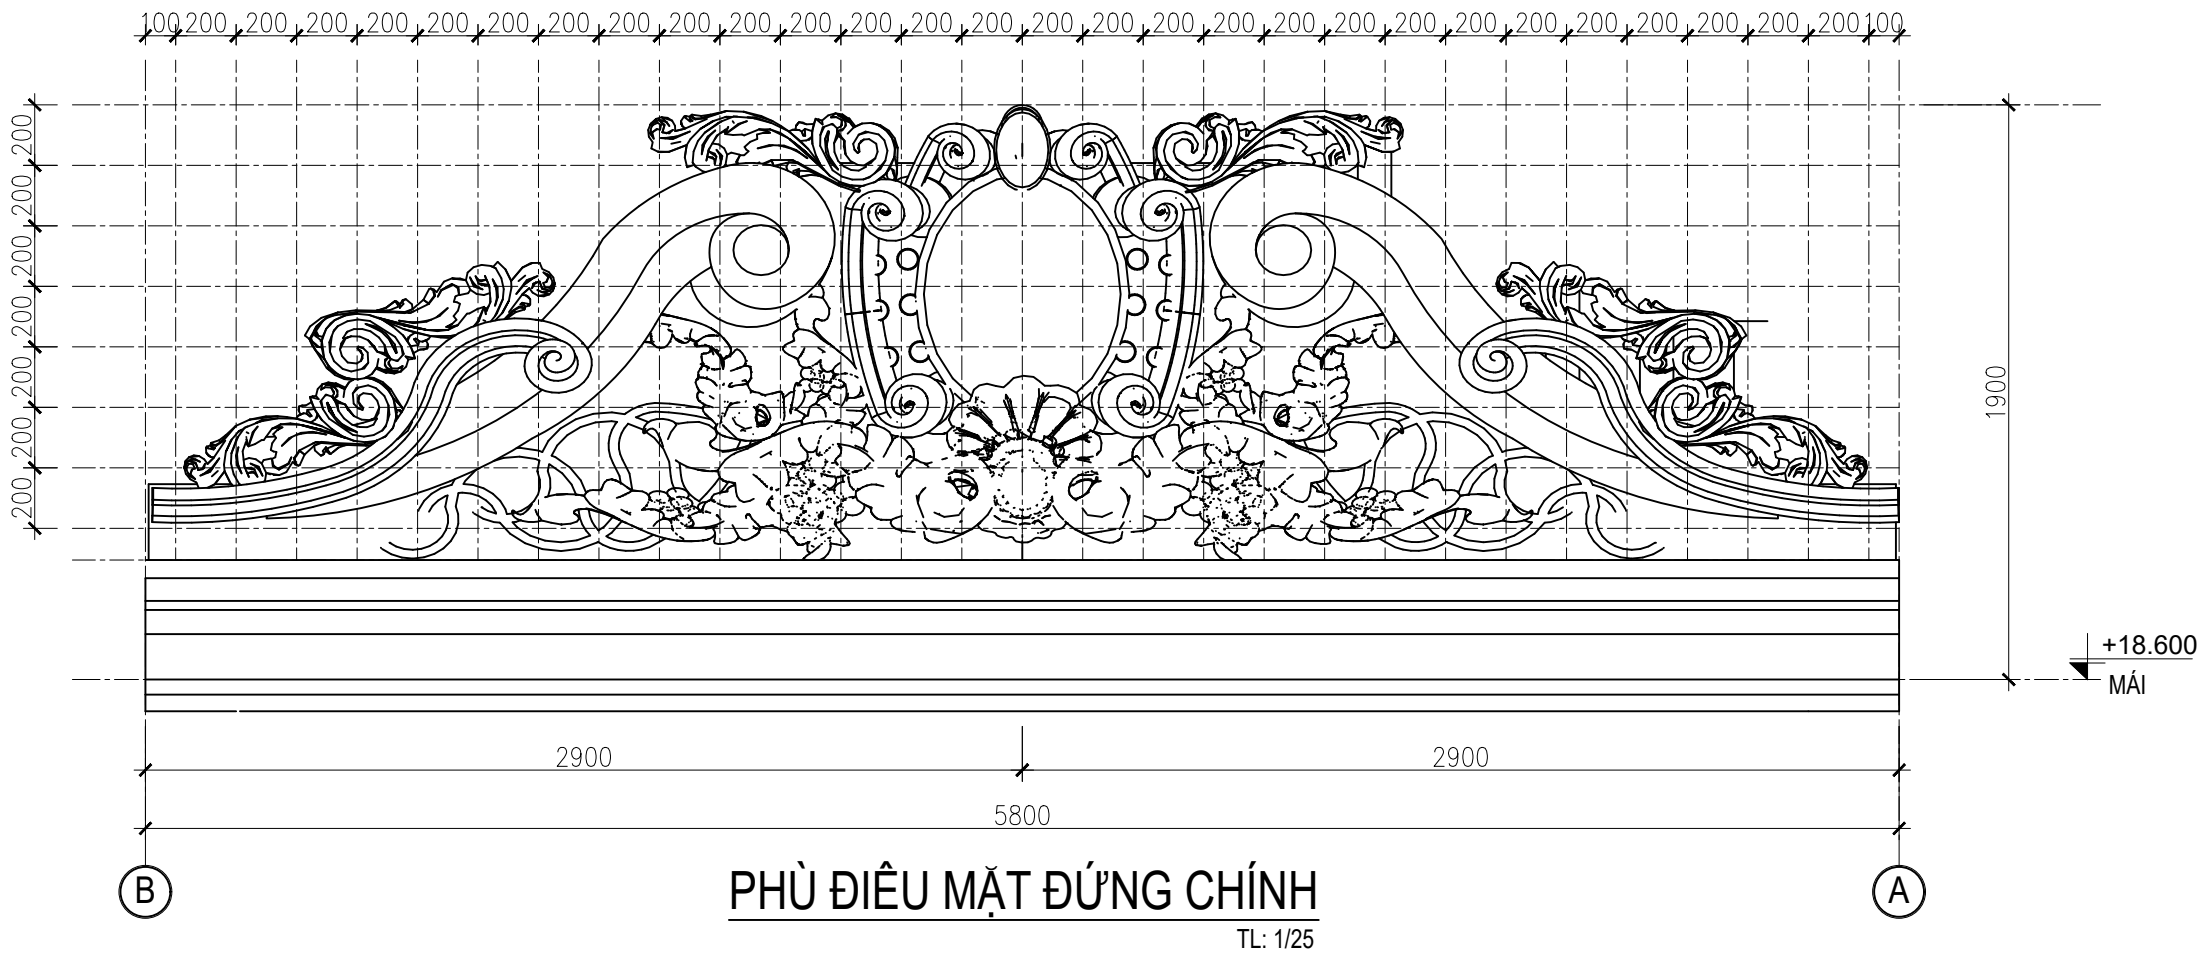

LOẠI HỒ SƠ / DOCUMENT STYPE

Thiết kế thi công (LOD 350)

Toàn bộ hồ sơ thiết kế, bản vẽ, hình ảnh và các nội dung liên quan thuộc quyền sở hữu trí tuệ của Công ty PV Incons. Không được sao chép, sửa đổi, chuyển nhượng hoặc sử dụng cho bất kỳ mục đích nào khác ngoài dự án này mà không có sự đồng ý bằng văn bản của chủ sở hữu bản quyền.

CHỦ ĐẦU TƯ / INVESTOR:

NGUYỄN HỮU THỪA

ĐỊA CHỈ / ADDRESS:

198, CÁCH MẠNG THÁNG TÁM,
PHƯỜNG BÌNH THỦY, TP. CẦN THƠ



CÔNG TY TNHH THƯƠNG MẠI VÀ XÂY DỰNG
PV INCONS

Địa chỉ: Số 007, Đ. Lý Thái Tổ, KDC.
Hưng Phú I, Q. Cái Răng, TP. Cần Thơ
Điện thoại: (+84) 0772 194 789
Email: pvincons@gmail.com

No.	Description	Date

- Bản vẽ thiết kế này chỉ được sử dụng khi đã được đọc, hiểu và kiểm tra bởi kỹ sư có chuyên môn phù hợp.

- Trong quá trình thi công, nếu có bất kỳ sai khác nào giữa bản vẽ thiết kế và thực tế hiện trường, đơn vị thi công phải báo cáo kịp thời cho đơn vị thiết kế và chủ đầu tư để được xem xét, điều chỉnh và phê duyệt trước khi tiếp tục thi công. Mọi sự thay đổi không được phép sẽ không thuộc trách nhiệm của đơn vị thiết kế.

- Đơn vị thi công phải lập bản vẽ Shop Drawing (LOD 400) cho các chi tiết kỹ thuật và trình duyệt trước khi triển khai.

- Kích thước trong bản vẽ là kích thước hoàn thiện, khi thi công cần kết hợp các bản vẽ có liên quan.

CÔNG TRÌNH / PROJECT NAME:

**NHÀ Ở KẾT HỢP VĂN
PHÒNG LÀM VIỆC**

ĐỊA ĐIỂM / LOCATION:

198, CÁCH MẠNG THÁNG TÁM,
PHƯỜNG BÌNH THỦY, TP. CẦN THƠ


HẠNG MỤC / ITEM:

CẢI TẠO MẶT TIỀN

TÊN BẢN VẼ / DRAWING TITLE:


SHEETTITLE

SỐ HỢP ĐỒNG 09/2026/HĐTK	HOÀN THÀNH .../09/2026
TỶ LỆ / SCALE: 1:100	SỐ BẢN VẼ: KT-05 /...

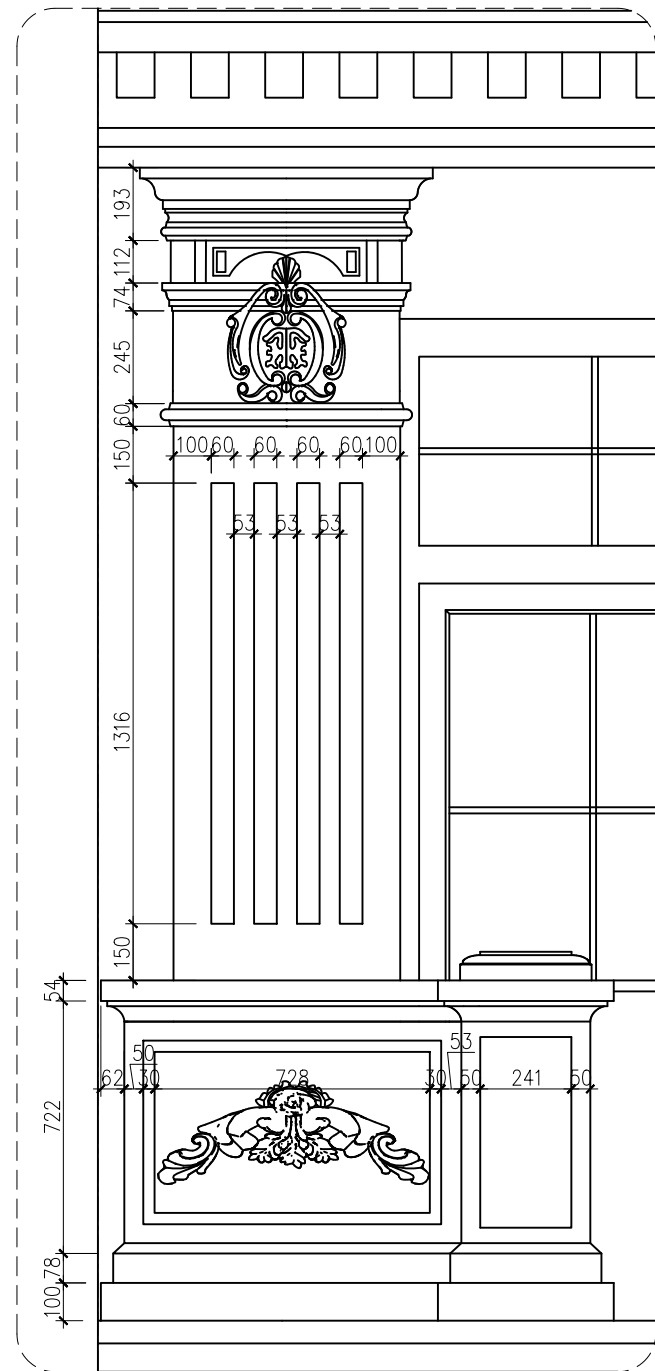

CHI TIẾT 1

TL: 1/20

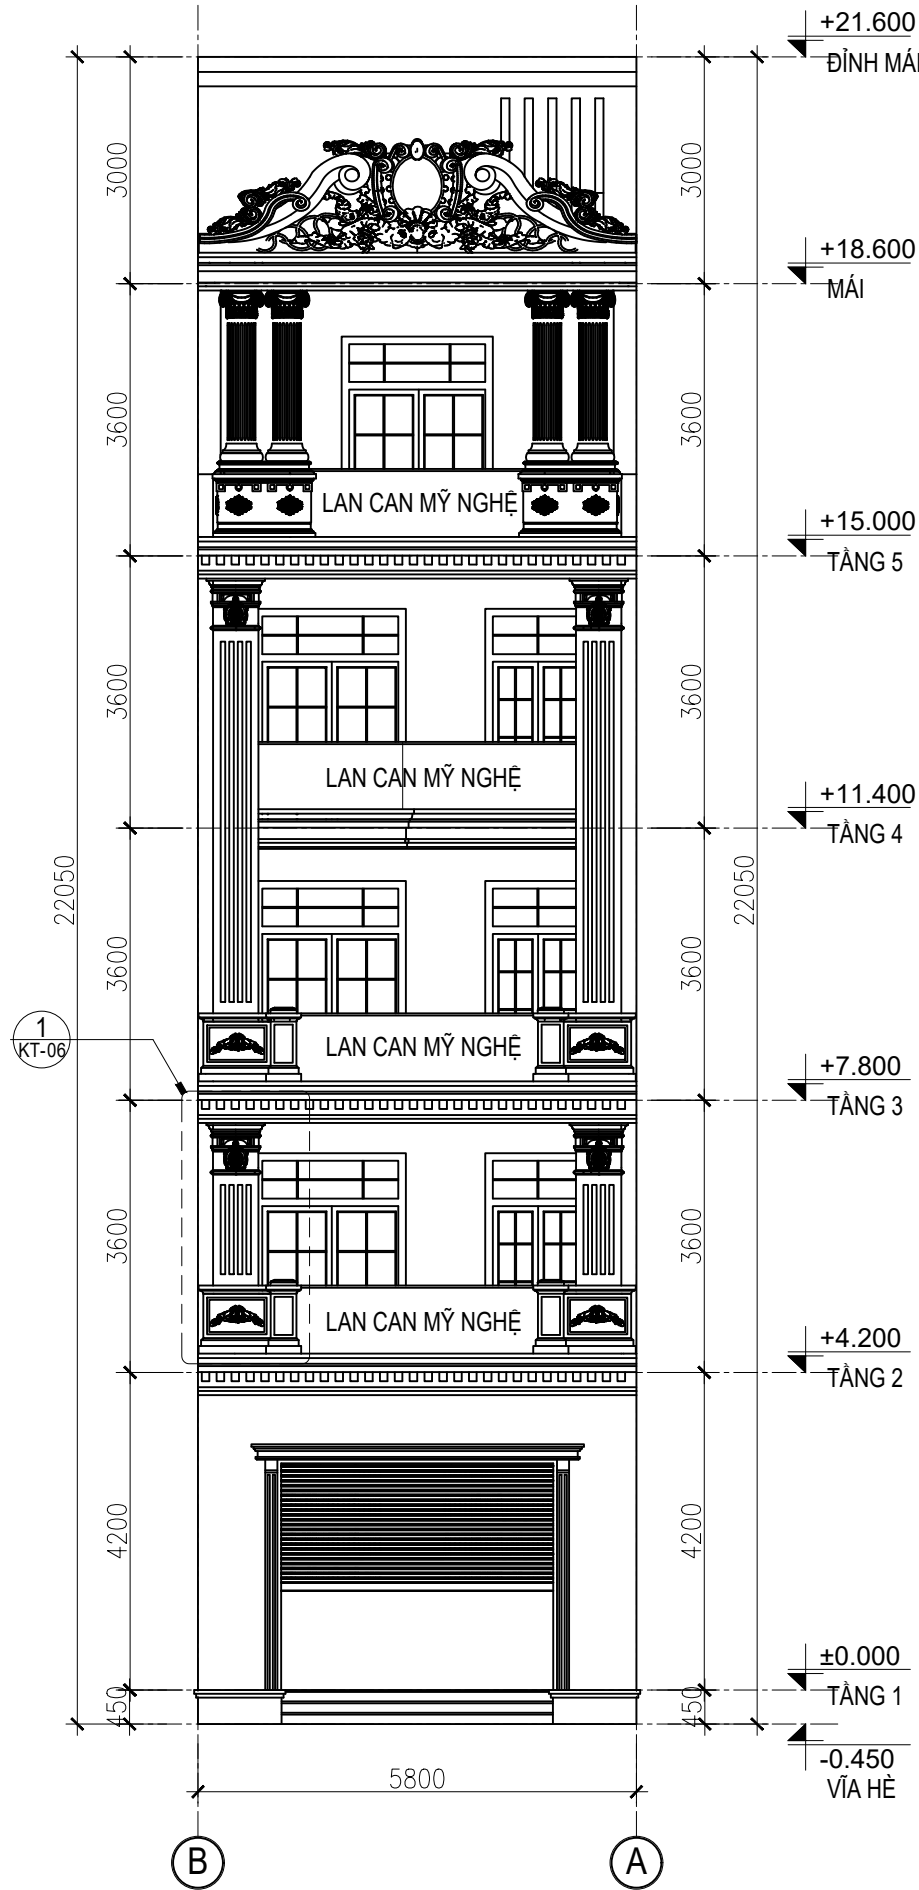

MẶT ĐỨNG TRỰC B-A

TL: 1/100

LOẠI HỒ SƠ / DOCUMENT STYPE

Thiết kế thi công (LOD 350)

Toàn bộ hồ sơ thiết kế, bản vẽ, hình ảnh và các nội dung liên quan thuộc quyền sở hữu trí tuệ của Công ty PV Incons. Không được sao chép, sửa đổi, chuyển nhượng hoặc sử dụng cho bất kỳ mục đích nào khác ngoài dự án này mà không có sự đồng ý bằng văn bản của chủ sở hữu bản quyền.

CHỦ ĐẦU TƯ / INVESTOR:

NGUYỄN HỮU THỪA

ĐỊA CHỈ / ADDRESS:

198, CÁCH MẠNG THÁNG TÁM,
PHƯỜNG BÌNH THỦY, TP. CẦN THƠ



CÔNG TY TNHH THƯƠNG MẠI VÀ XÂY DỰNG
PV INCONS

Địa chỉ: Số 007, Đ. Lý Thái Tổ, KDC.

Hưng Phú I, Q. Cái Răng, TP. Cần Thơ

Điện thoại: (+84) 0772 194 789

Email: pvincons@gmail.com

No.	Description	Date

- Bản vẽ thiết kế này chỉ được sử dụng khi đã được đọc, hiểu và kiểm tra bởi kỹ sư có chuyên môn phù hợp.

- Trong quá trình thi công, nếu có bất kỳ sai khác nào giữa bản vẽ thiết kế và thực tế hiện trường, đơn vị thi công phải báo cáo kịp thời cho đơn vị thiết kế và chủ đầu tư để được xem xét, điều chỉnh và phê duyệt trước khi tiếp tục thi công. Mọi sự thay đổi không được phép sẽ không thuộc trách nhiệm của đơn vị thiết kế.

- Đơn vị thi công phải lập bản vẽ Shop Drawing (LOD 400) cho các chi tiết kỹ thuật và trình duyệt trước khi triển khai.

- Kích thước trong bản vẽ là kích thước hoàn thiện, khi thi công cần kết hợp các bản vẽ có liên quan.

CÔNG TRÌNH / PROJECT NAME:

NHÀ Ở KẾT HỢP VĂN
PHÒNG LÀM VIỆC

ĐỊA ĐIỂM / LOCATION:

198, CÁCH MẠNG THÁNG TÁM,
PHƯỜNG BÌNH THỦY, TP. CẦN THƠ

HANG MỤC / ITEM:

CẢI TẠO MẶT TIỀN

TÊN BẢN VẼ / DRAWING TITLE:

SHEETTITLE

SỐ HỢP ĐỒNG
09/2026/HĐTK


HOÀN THÀNH
.../09/2026

TỶ LỆ / SCALE:


SỐ BẢN VẼ:

1:100

KT-06 /...

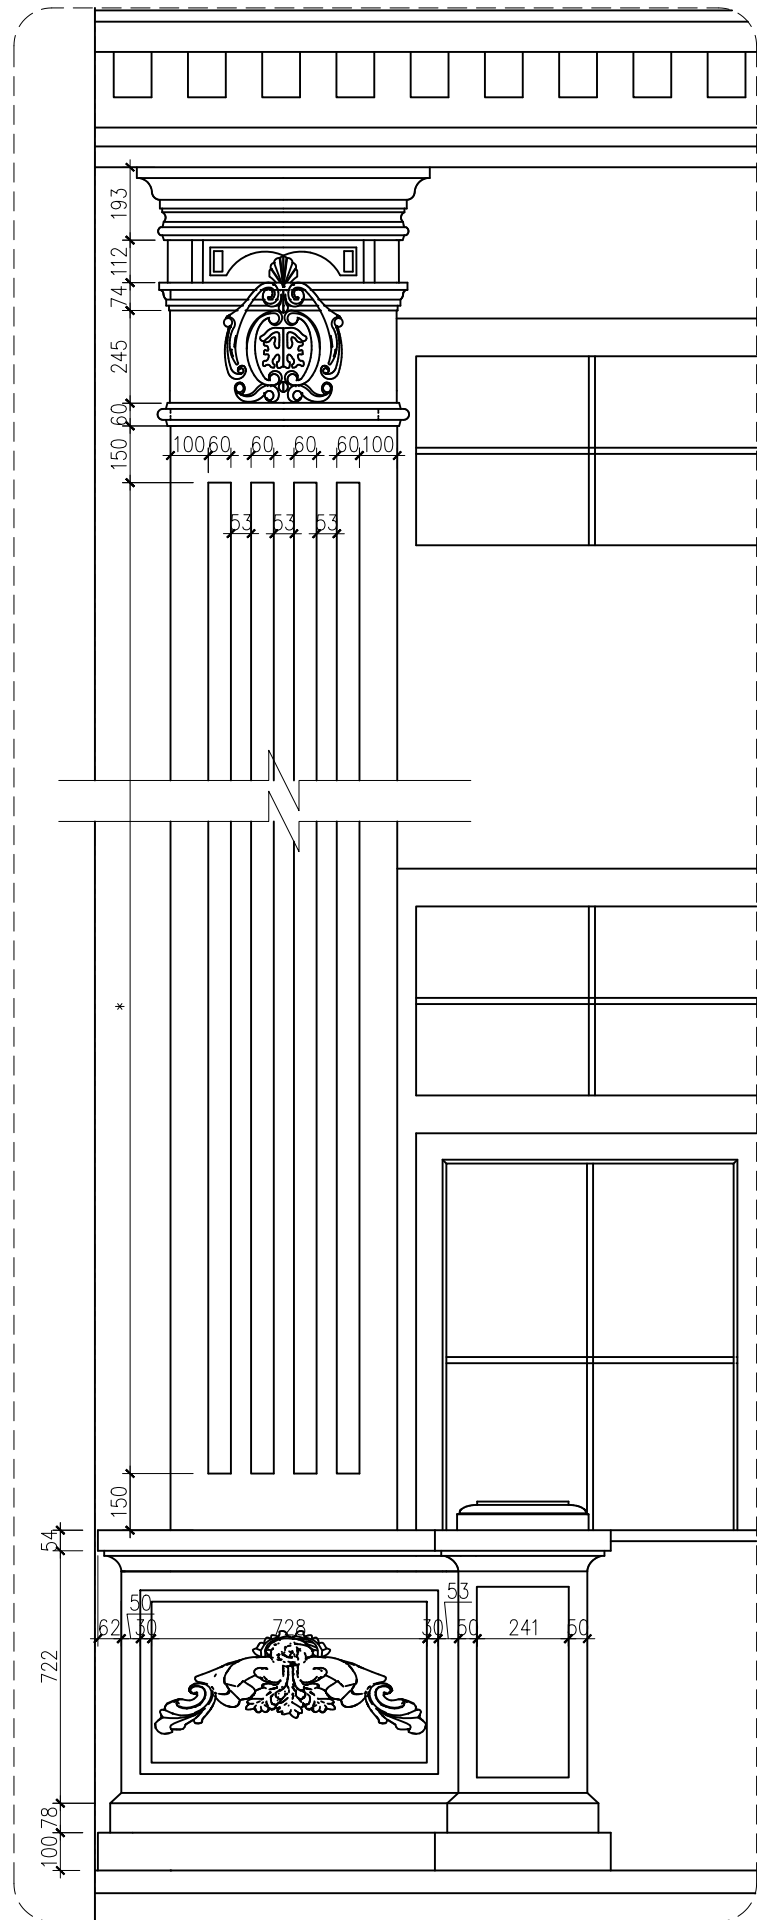

CHI TIẾT 2
TL: 1/20

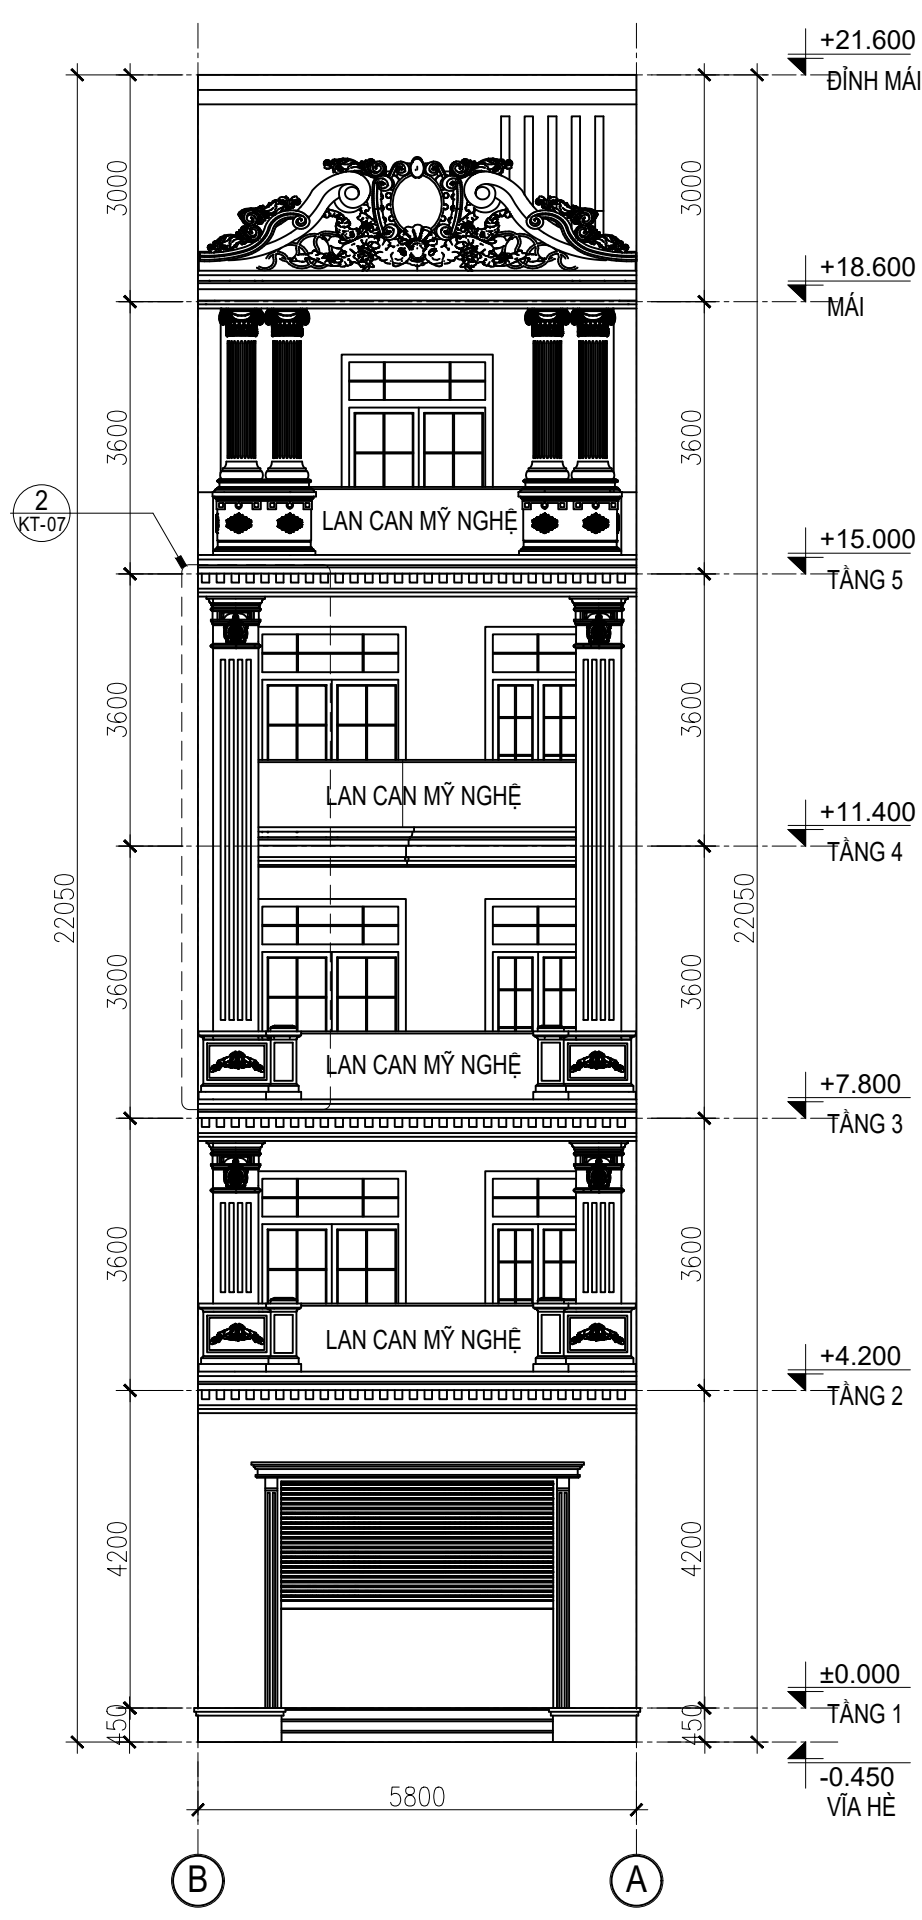

MẶT ĐỨNG TRỤC B-A
TL: 1/100

LOẠI HỒ SƠ / DOCUMENT STYPE

Thiết kế thi công (LOD 350)

Toàn bộ hồ sơ thiết kế, bản vẽ, hình ảnh và các nội dung liên quan thuộc quyền sở hữu trí tuệ của Công ty PV Incons. Không được sao chép, sửa đổi, chuyển nhượng hoặc sử dụng cho bất kỳ mục đích nào khác ngoài dự án này mà không có sự đồng ý bằng văn bản của chủ sở hữu bản quyền.

CHỦ ĐẦU TƯ / INVESTOR:

NGUYỄN HỮU THỪA

ĐỊA CHỈ / ADDRESS:

198, CÁCH MẠNG THÁNG TÁM, PHƯỜNG BÌNH THỦY, TP. CẦN THƠ



CÔNG TY TNHH THƯƠNG MẠI VÀ XÂY DỰNG

PV INCONS

Địa chỉ: Số 007, Đ. Lý Thái Tổ, KDC. Hưng Phú I, Q. Cái Răng, TP. Cần Thơ

Điện thoại: (+84) 0772 194 789

Email: pvincons@gmail.com

No.	Description	Date

- Bản vẽ thiết kế này chỉ được sử dụng khi đã được đọc, hiểu và kiểm tra bởi kỹ sư có chuyên môn phù hợp.

- Trong quá trình thi công, nếu có bất kỳ sai khác nào giữa bản vẽ thiết kế và thực tế hiện trường, đơn vị thi công phải báo cáo kịp thời cho đơn vị thiết kế và chủ đầu tư để được xem xét, điều chỉnh và phê duyệt trước khi tiếp tục thi công. Mọi sự thay đổi không được phép sẽ không thuộc trách nhiệm của đơn vị thiết kế.

- Đơn vị thi công phải lập bản vẽ Shop Drawing (LOD 400) cho các chi tiết kỹ thuật và trình duyệt trước khi triển khai.

- Kích thước trong bản vẽ là kích thước hoàn thiện, khi thi công cần kết hợp các bản vẽ có liên quan.

CÔNG TRÌNH / PROJECT NAME:

NHÀ Ở KẾT HỢP VĂN PHÒNG LÀM VIỆC

ĐỊA ĐIỂM / LOCATION:

198, CÁCH MẠNG THÁNG TÁM, PHƯỜNG BÌNH THỦY, TP. CẦN THƠ

HẠNG MỤC / ITEM:

CẢI TẠO MẶT TIỀN


TÊN BẢN VẼ / DRAWING TITLE:

SHEETTITLE

SỐ HỢP ĐỒNG	HOÀN THÀNH
09/2026/HĐTK	.../09/2026
TỶ LỆ / SCALE:	SỐ BẢN VẼ:
1:100	KT-07 /...

[illegible]


CÔNG TRÌNH / PROJECT NAME:	
NHÀ Ở KẾT HỢP VĂN PHÒNG LÀM VIỆC	
ĐỊA ĐIỂM / LOCATION:	
198, CÁCH MẠNG THÁNG TÁM, PHƯỜNG BÌNH THỦY, TP. CẦN THƠ	
HẠNG MỤC / ITEM:	
CẢI TẠO MẶT TIỀN	
TÊN BẢN VẼ / DRAWING TITLE:	
SHEETTITLE	
SỐ HỢP ĐỒNG 09/2026/HĐTK	HOÀN THÀNH .../09/2026
TỶ LỆ / SCALE: 1:100	SỐ BẢN VẼ: KT-08 /...

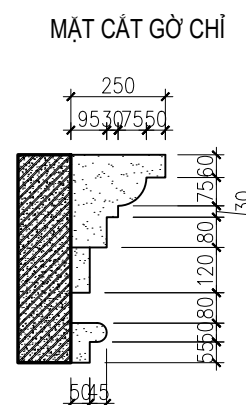

Technical drawing of a symmetrical architectural element, labeled (B). The drawing shows a cross-section of a structure with a total width of 2900. The structure is symmetrical, as indicated by the "ĐỐI XỨNG" (Symmetrical) label and the dashed line. The vertical dimensions on the right side are: 55, 50, 150, 80, 175, and 60. The drawing includes a dashed line indicating the center of symmetry and a dashed line indicating the top edge of the structure.

MẶT CẮT GỜ CHÌ

250
20 75 50 75 55
250
70
80 150 50
60 45 55

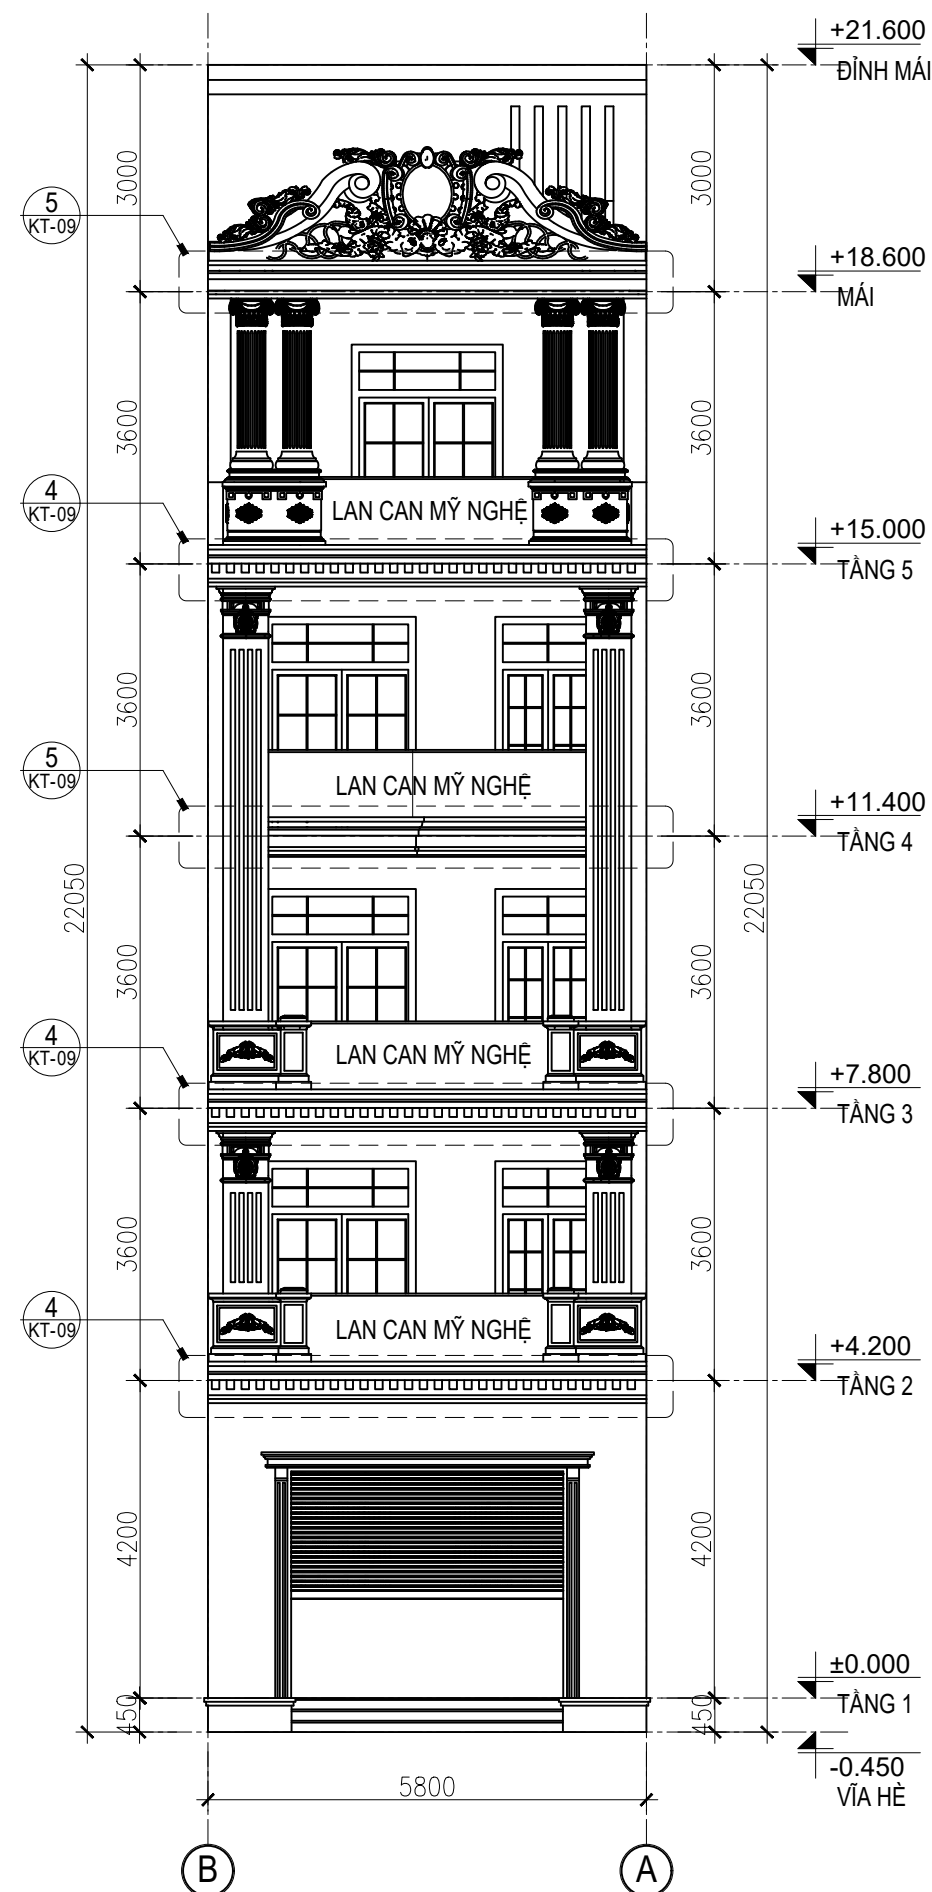

LOẠI HỒ SƠ / DOCUMENT STYPE
Thiết kế thi công (LOD 350)

Toàn bộ hồ sơ thiết kế, bản vẽ, hình ảnh và các nội dung liên quan thuộc quyền sở hữu trí tuệ của Công ty PV Incons. Không được sao chép, sửa đổi, chuyển nhượng hoặc sử dụng cho bất kỳ mục đích nào khác ngoài dự án này mà không có sự đồng ý bằng văn bản của chủ sở hữu bản quyền.

CHỦ ĐẦU TƯ / INVESTOR:

NGUYỄN HỮU THỪA

ĐỊA CHỈ / ADDRESS:
198, CÁCH MẠNG THÁNG TÁM,
PHƯỜNG BÌNH THỦY, TP. CẦN THƠ



CÔNG TY TNHH THƯƠNG MẠI VÀ XÂY DỰNG
PV INCONS

Địa chỉ: Số 007, Đ. Lý Thái Tổ, KDC
Hưng Phú I, Q. Cái Răng, TP. Cần Thơ
Điện thoại: (+84) 0772 194 789
Email: pvincons@gmail.com

No.	Description	Date

- Bản vẽ thiết kế này chỉ được sử dụng khi đã được đọc, hiểu và kiểm tra bởi kỹ sư có chuyên môn phù hợp.

- Trong quá trình thi công, nếu có bất kỳ sai khác nào giữa bản vẽ thiết kế và thực tế hiện trường, đơn vị thi công phải báo cáo cấp thời cho đơn vị thiết kế và chủ đầu tư để được xem xét, điều chỉnh và phê duyệt trước khi tiếp tục thi công. Mọi sự thay đổi không được phép sẽ không thuộc trách nhiệm của đơn vị thiết kế.

- Đơn vị thi công phải lập bản vẽ Shop Drawing (LOD 400) cho các chi tiết kỹ thuật và trình duyệt trước khi triển khai.

- Kích thước trong bản vẽ là kích thước hoàn thiện, khi thi công cần kết hợp các bản vẽ có liên quan.

CÔNG TRÌNH / PROJECT NAME:

NHÀ Ở KẾT HỢP VĂN PHÒNG LÀM VIỆC

ĐỊA ĐIỂM / LOCATION:
198, CÁCH MẠNG THÁNG TÁM,
PHƯỜNG BÌNH THỦY, TP. CẦN THƠ

HANG MỤC / ITEM:

CẢI TẠO MẶT TIỀN

TÊN BẢN VẼ / DRAWING TITLE:

SHEETTITLE

SỐ HỢP ĐỒNG 09/2026/HĐTK	HOÀN THÀNH .../09/2026
TỶ LỆ / SCALE: 1:100	SỐ BẢN VẼ: KT-09 /...